
# 擁壁 平面割付図　S=1/100

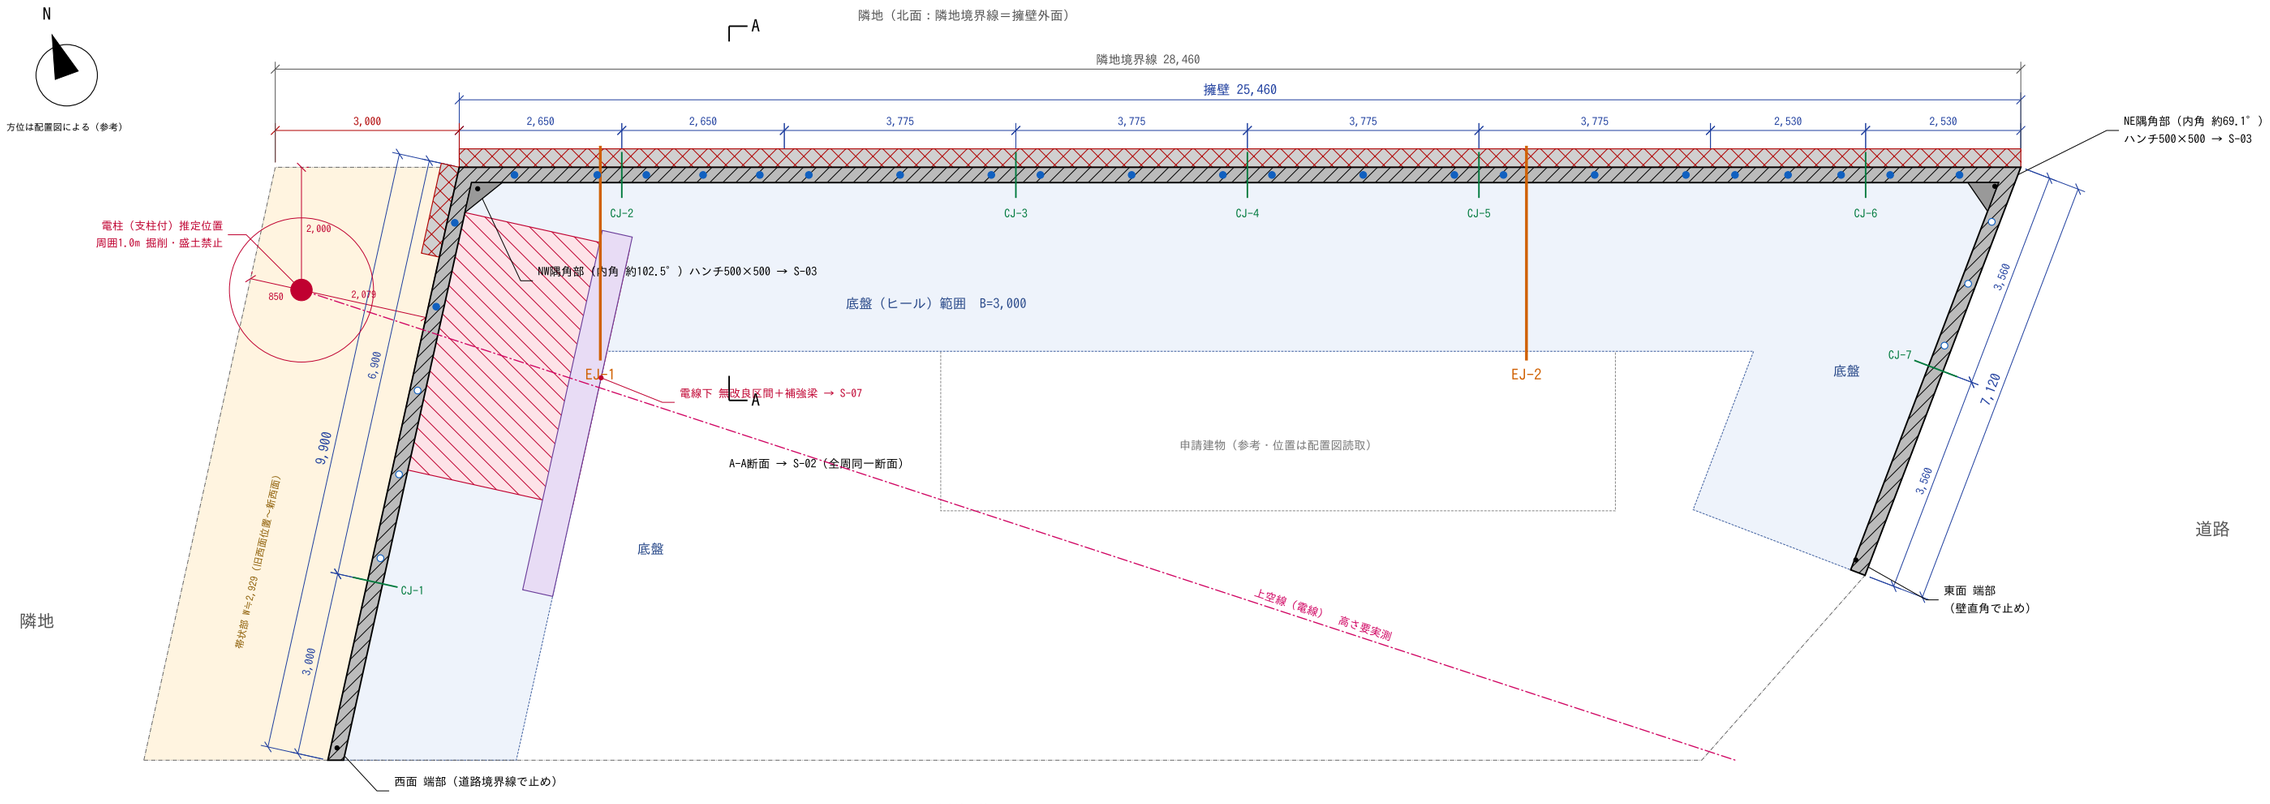


## 目地・水抜穴 割付表（寸法は擁壁外面＝境界線に沿う）

| 面 | 延長 | 誘発目地 CJ 位置 | 伸縮目地 EJ 位置 | 水抜穴 |
|---|---|---|---|---|
| 西面 | 9,900 | NW隅から 6,900 | — | 5 箇所 |
| 北面 | 25,460 | NW隅から 2,650 / 9,075 / 12,850 / 16,625 / 22,930 | NW隅から 5,300 / 20,400 | 22 箇所 |
| 東面 | 7,120 | NE隅から 3,560 | — | 3 箇所 |
| 計 | 42,480 | 7 箇所 | 2 箇所 | 30 箇所 |

## 水抜穴 位置表（隅角部からの距離 / 芯高さ ±0基準）

西面（NW隅→南）：　900 / 2,300 / 3,700[-950] / 5,100[-750] / 6,500[-550] / 7,300(省略) / 8,400(省略) / 9,500(省略)

北面（NW隅→東）：　900 / 2,250 / 3,050 / 3,975 / 4,900 / 5,700 / 7,188 / 8,675 / 9,475 / 10,963 / 12,450 / 13,250 / 14,738 / 16,225 / 17,025
18,512 / 20,000 / 20,800 / 21,665 / 22,530 / 23,330 / 24,460

東面（NE隅→南）：　1,000[-800] / 2,080[-650] / 3,160[-500] / 3,960(省略) / 5,340(省略) / 6,720(省略)

※無印＝標準高さ GL-1060（止水コン天端に管底）。[ ]内＝調整高さ（外部地盤+150）。(省略)＝外部地盤が高く排水不可のため設けない。
※外部地盤は配置図からの読取値。墨出し時に外部地盤高さを実測し、右記ルールで最終高さを決定すること。

## 凡例


- 立上り t=250
- 底盤 B3000 t500
- EJ 伸縮目地
- CJ 誘発目地
- 水抜穴 標準高さ
- 水抜穴 高さ調整
- 前面ふかしコン

## 特記事項

1. 北面・東面の擁壁外面＝隣地／道路境界線。西面は境界から敷地側へ
   北面に沿って 3,000 移動（境界と平行、直角離れ 2,929）。NW隅＝新隅角。
2. 壁角度は配置図読取値（NW隅 約102.5° ・NE隅 約69.1°）。
   境界杭にて現地確認のうえ墨出しすること。
3. 伸縮目地 EJ：全断面（立上り＋底盤）縁切り、
   区間長 15.2m／15.1m／12.2m（≦20m）、隅角部から2m以上離す。
4. 誘発目地 CJ：立上り両面に目地棒、間隔 4.1m以内。
5. 水抜穴：VP75（内径75以上）、1.5m以内ピッチ
   （露出面 約1.9m²/箇所 ≦3m²）、外部へ2%以上の勾配。
   高さルール：外部地盤 ≦GL-1210 → GL-1060(標準)
   GL-1210～-650 → 外部地盤+150
   GL-650 超 → 設けない
6. 隅角部（2箇所）はハンチ500×500＋補強筋（S-03）。
7. 断面・配筋は S-02、目地・隅角・端部詳細は S-03、
   展開図は S-04、鉄筋加工帳・数量は S-05 による。
8. 根入れ：北面全長・西面NW隅から1.5mは前面地盤を ±0-1500 に
   嵩上げ＋前面ふかしコン W300（無筋）で根入れ400を確保。
9. 電柱（推定位置）：西境界から850・北境界から2,000。新西面外面まで
   芯で約2,079（表面で約1,904≧1,000）。電柱・支柱の位置は
   着工前に実測。周囲1.0mは掘削・盛土禁止。施工検討は S-06。
10. 電線下で柱状改良を打てない区間（西面 NW隅から700～5,000）は
    底盤補強＋ヒール端補強梁で両側の改良区間へ架け渡す（S-07）。
11. 【VE・改3-2】解体ガラ（土間コン・ブロック）と割栗石は処分せず場内で再利用。
    裏込め砕石の外側の水はけ層（S-02）・西／東面ヒール上の埋戻し下層・帯状部・
    北側嵩上げの下層。北面ヒール上（建物の下）には使わない。構造設計者の承認後。

| | | | | | | |
|---|---|---|---|---|---|---|
| 工事名<br>大信薬局様邸新築工事 | ハゼモト建設株式会社<br>一級建築士事務所<br>北九州市小倉北区片野4-12-10　TEL 093-931-0521　FAX 093-931-0927 | 管理者<br>檜本 健一 | 設計者 | 担当者 | 図面名<br>擁壁 平面割付図 | 図面No<br>S-01 |
| 備考<br>鉄筋・型枠・土工 協力業者配布用<br>改3-2 2026/11/14 電柱側 矢板なし（S-06）・ガラ／割栗石の場内再利用（VE）／改3-1 11/11 電線下補強 | | 日付<br>2026/11/14 | 日付 | 日付 | 縮尺<br>1/100 | 施工図 |

# 擁壁 標準断面配筋図（A-A 全周共通）　S=1/20

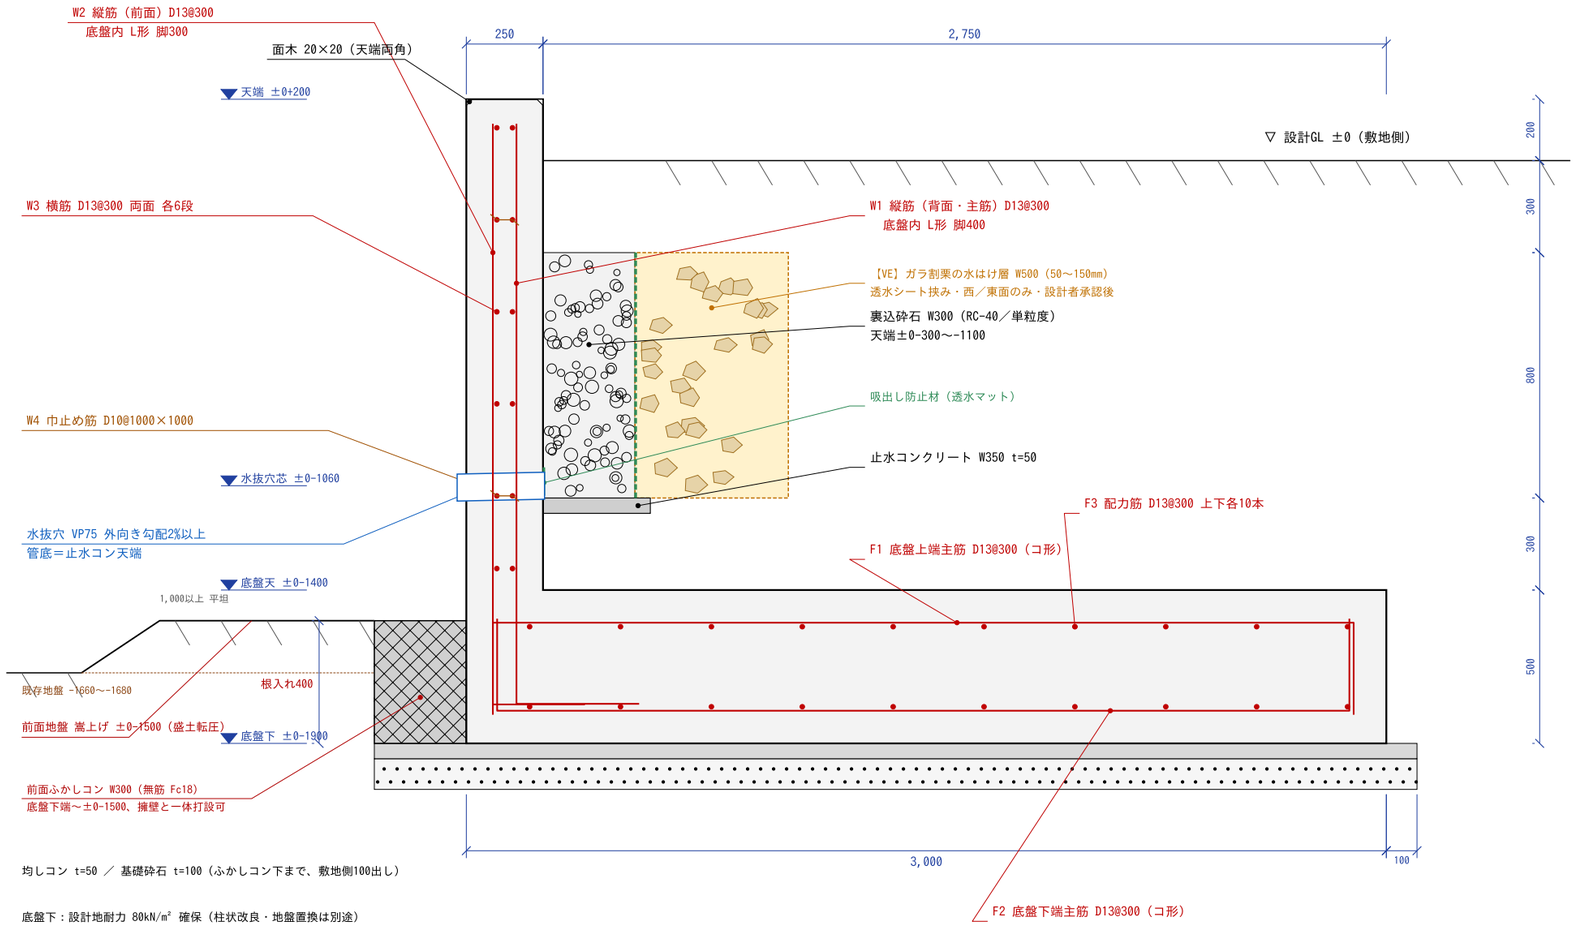


均しコン t=50 ／ 基礎砕石 t=100（ふかしコン下まで、敷地側100出し）


底盤下：設計地耐力 80kN/m² 確保（柱状改良・地盤置換は別途）

## 設計条件・配筋特記


設計地耐力 80kN/m²　地表面積載荷重 10kN/m²
コンクリート Fc=21N/mm²（呼び強度は構造体補正 mSn を加算）
鉄筋 SD295　かぶり厚さ：壁 80 ／ 底盤 100（全面）
重ね継手 40d（D13＝520）千鳥継手　定着 35d（フック付 25d）
スペーサー：壁 80用 縦横@1,000以内／底盤 サイコロ100 @1,000以内
打継ぎ：底盤天で水平打継ぎ。レイタンス除去・目荒らし後に立上り打設。
縦筋は先組し底盤と同時に固定、打設時に移動させないこと。
縦筋は前面・背面とも 外側、横筋は内側に配筋（有効せい確保）。

## 部分詳細　S=1/10

① 天端（面木）

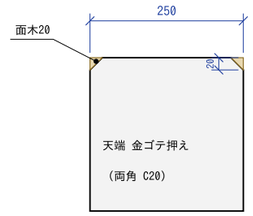



② 誘発目地 CJ（平面）

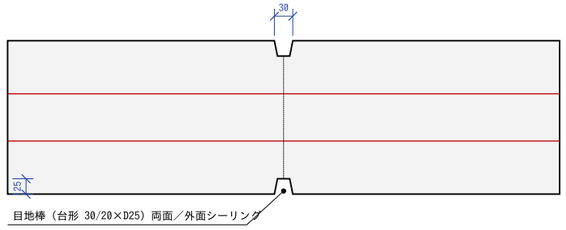


断面欠損 50/250＝20%　横筋は連続
範囲：天端～底盤天（立上り部のみ）


③ 水抜穴（断面）

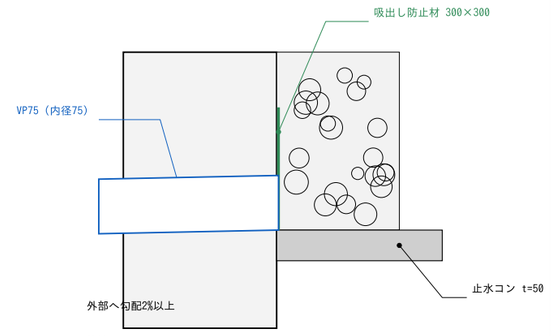


| | | | | | | |
|---|---|---|---|---|---|---|
| 工事名<br>大信薬局様邸新築工事 | ハゼモト建設株式会社<br>一級建築士事務所<br>北九州市小倉北区片野4-12-10　TEL 093-931-0521　FAX 093-931-0927 | 管理者<br>檜本 健一 | 設計者 | 担当者 | 図面名<br>擁壁 標準断面配筋図 | 図面No<br>S-02 |
| 備考<br>鉄筋・型枠・土工 協力業者配布用<br>改3-2 2026/11/14 電柱側 矢板なし（S-06）・ガラ／割栗石の場内再利用（VE）／改3-1 11/11 電線下補強 | | 日付<br>2026/11/14 | 日付 | 日付 | 縮尺<br>1/20・1/10 | 施工図 |


# 伸縮目地・誘発目地・隅角部・端部 詳細

## ① 伸縮目地 EJ（平面） S=1/10

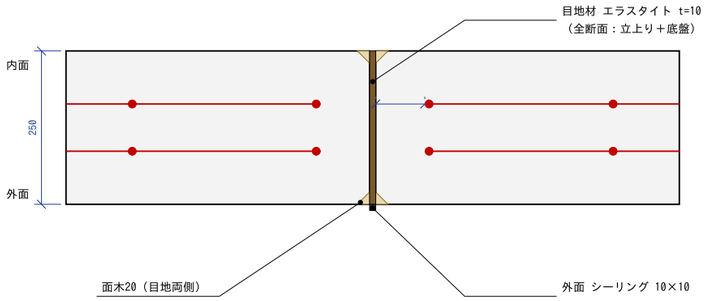



・鉄筋は目地で切断（目地面かぶり 壁80／底盤100）
・底盤も同位置で縁切り。妻型枠を立て片側ずつ打設
・天端・外面の目地際は面木20で面取り
・位置：北面 NW隅から 5,300 ／ 20,400（S-01）
・改3：NW隅＝新西面と北面の交点（境界NW角から東へ3,000）

## ② 誘発目地 CJ（立面・外面） S=1/30

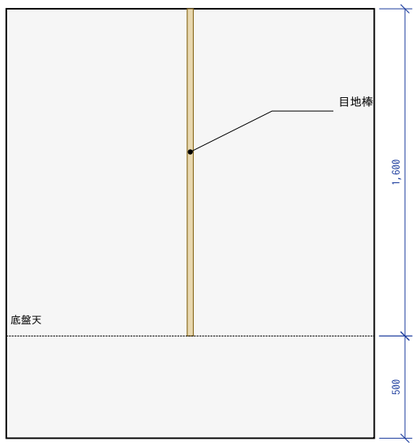



・目地棒 台形 30/20×D25（木製又は樹脂製）
　立上り 両面、天端～底盤天まで通す
・天端は目地位置で V カット 10
・断面欠損 50/250＝20%、横筋は連続
・外面側目地にシーリング 10×10
・底盤部は連続（目地を設けない）

## ③ NW隅角部（平面） S=1/30　内角 約102.5°

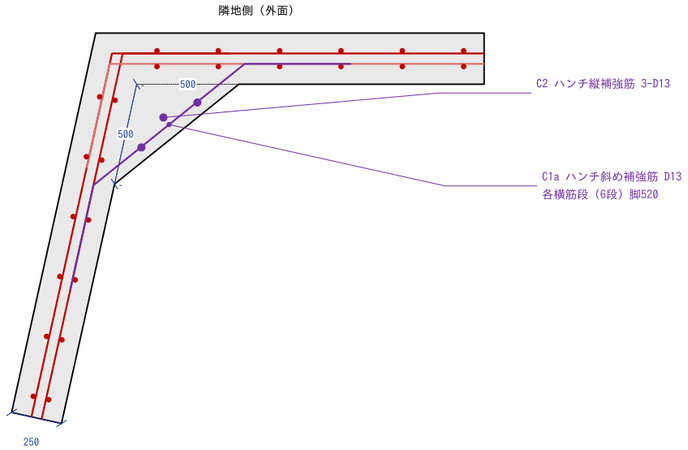



## ④ NE隅角部（平面） S=1/30　内角 約69.1°

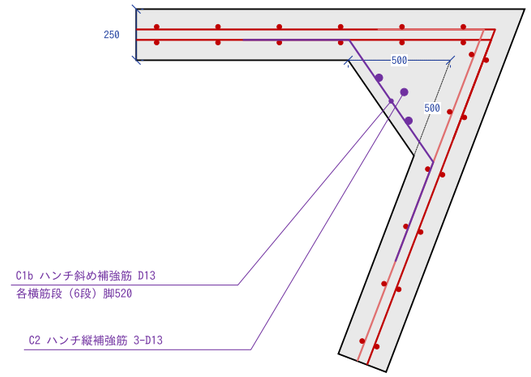


【隅角部 共通】
・外面側横筋：隅角部で折曲げ連続（継手を設けない。やむを得ない場合は重ね520）
・内面側横筋：相手壁の外面側横筋位置まで延ばし、折曲げて 520 定着（C3）
・ハンチ：二等辺三角形 500×500（宅地防災マニュアル H≦3m）、天端～底盤天まで全高
・底盤：隅角部は両方向の主筋・配力筋を重ねて配置し一体打設
・伸縮目地・誘発目地は隅角部から2m以上離す（S-01割付済）
・NE隅は鋭角（約69°）：出隅に面木20、鋭角部のかぶり80を必ず確保


## ⑤ 壁端部（平面） S=1/20

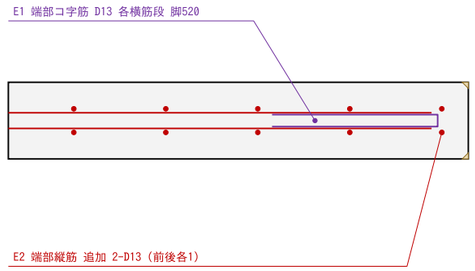



・西面端部：道路境界線に沿って止め
・東面端部：壁に直角に止め
・端部の鉛直出隅は面木20
・底盤端部は配力筋を90°フック（余長300）

| | | | | | |
|---|---|---|---|---|---|
| 工事名<br>大信薬局様邸新築工事 | ハゼモト建設株式会社<br>一級建築士事務所<br>北九州市小倉北区片野4-12-10 TEL 093-931-0521 FAX 093-931-0927 | 管理者<br>檜本 健一 | 設計者 | 担当者 | 図面名<br>擁壁 目地・隅角部・端部詳細 | 図面No<br>S-03 |
| 備考<br>鉄筋・型枠・土工 協力業者配布用<br>改3-2 2026/11/14 電柱側 矢板なし（S-06）・ガラ／割栗石の場内再利用（VE）／改3-1 11/11 電線下補強 | | 日付<br>2026/11/14 | 日付 | 日付 | 縮尺<br>1/10・1/20・1/30 | 施工図 |

# 擁壁 展開図（敷地内側より見る）　S=1/60　※水抜穴は外面まで貫通

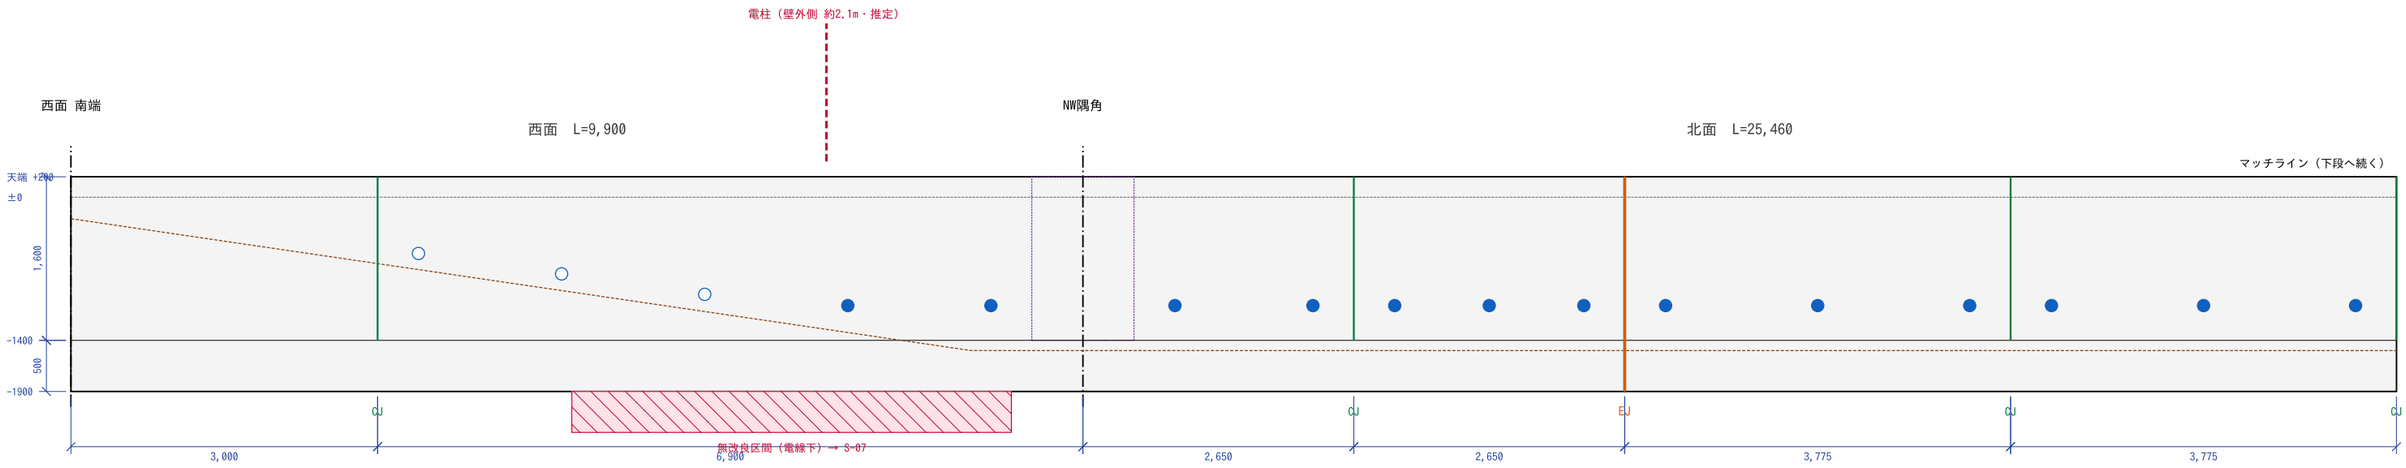

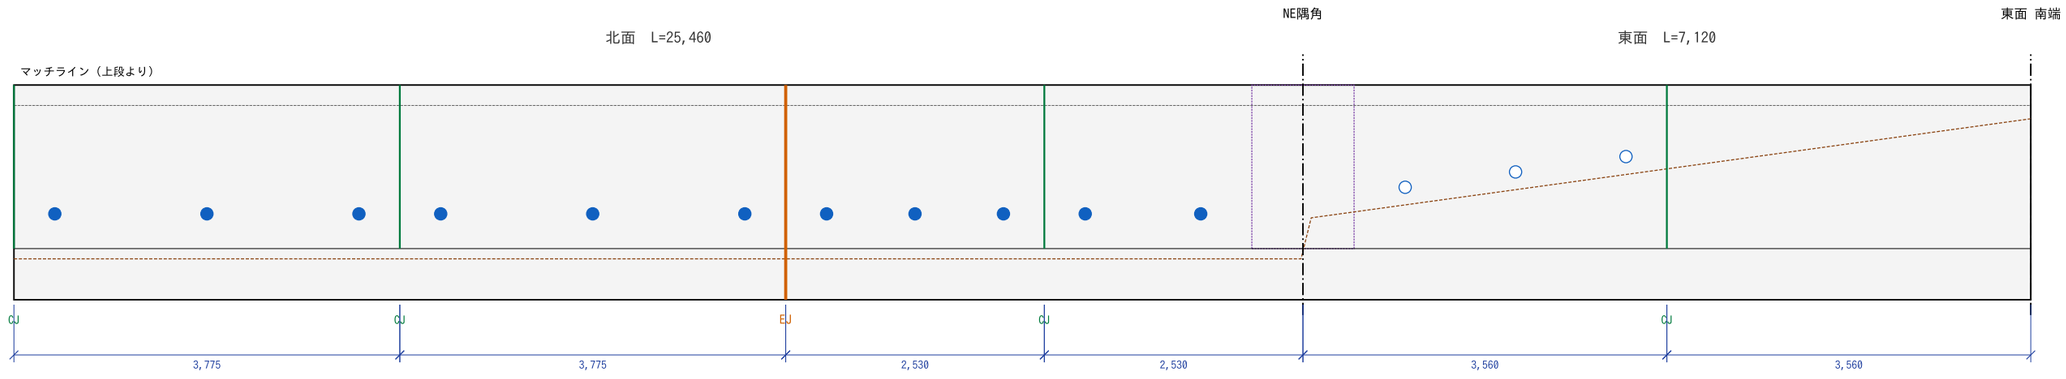
## 凡例・注記

| | |
|---|---|
| EJ | 伸縮目地：底盤まで全断面縁切り（エラスタイト t=10＋外面シーリング） |
| CJ | 誘発目地：立上り両面 目地棒 30/20×D25（天端～底盤天） |
| ● | 水抜穴 VP75 標準高さ ±0-1060（管底＝止水コン天端） |
| ○ | 水抜穴 調整高さ＝外部地盤+150（止水コンも同高さに上げる） |
| - - | 外部地盤（嵩上げ後）：北 -1500（既存-1660～-1680を嵩上げ）／西（帯状部・仮定）NW隅1.5mまで-1500→南端-210／東 -1110→-130 |
| □ | 隅角部ハンチ 500×500 範囲 |

・天端は ±0+200 で水平（各点の現況GL：A-1/B-1 +57, B-3 +60, B-4 +50, B-5 +100, C-1 ±0, D-1 +25）。
・底盤下端 ±0-1900 で水平。BMは配置図 ±0 とし、着工前にレベル確認。
・型枠：北面・東面の外面は境界線上。外部側作業スペースは隣地・道路管理者と事前協議。
・西面は境界から2,929内側（改3）。外面側の帯状部に電柱あり：電柱周囲1.0mは掘削・盛土・資材仮置き禁止（S-06）。
・型枠締付け：セパレーター＋Pコン（外面はPコン穴モルタル充填）。
・水抜穴は型枠に VP75 を仕込み、外部へ 2% 以上の下り勾配で固定。

| | | | | | | |
|---|---|---|---|---|---|---|
| 工事名<br>大信薬局様邸新築工事 | ハゼモト建設株式会社<br>一級建築士事務所<br>北九州市小倉北区片野4-12-10　TEL 093-931-0521　FAX 093-931-0927 | 管理者<br>櫨本 健一 | 設計者 | 担当者 | 図面名<br>擁壁 展開図 | 図面No<br>S-04<br>施工図 |
| 備考<br>鉄筋・型枠・土工 協力業者配布用<br>改3-2 2026/11/14 電柱側 矢板なし（S-06）・ガラ／割栗石の場内再利用（VE）／改3-1 11/11 電線下補強 | | 日付<br>2026/11/14 | 日付 | 日付 | 縮尺<br>1/60 | |

# 鉄筋加工帳（D13・D10 SD295／D19 SD345）

| 符号 | 名称 | 径 | 形状 | 加工寸法(mm) | 1本長 | 本数 | 総長m | 重量kg | 備考 |
|---|---|---|---|---|---|---|---|---|---|
| W1 | 壁縦筋（背面・主筋） | D13 | L形 | 1890+400 | 2,290 | 142 | 325.2 | 324 | @300 |
| W2 | 壁縦筋（前面） | D13 | L形 | 1890+300 | 2,190 | 142 | 311.0 | 309 | @300 |
| W3 | 壁横筋（両面×6段） | D13 | 直 | 定尺6.0m | 5,968 | 97 | 578.9 | 576 | 継手72箇所（40d） |
| W4 | 巾止め筋 | D10 | S形 | 90+フック | 300 | 74 | 22.2 | 12 | @1000×1000 |
| F1 | 底盤上端主筋 | D13 | コ形(下向) | 300+2787+300 | 3,387 | 142 | 481.0 | 479 | @300 |
| F2 | 底盤下端主筋 | D13 | コ形(上向) | 300+2759+300 | 3,359 | 142 | 477.0 | 475 | @300 |
| F3 | 底盤配力筋（上下×10本） | D13 | 直 | 定尺6.0m | 5,993 | 161 | 964.8 | 960 | 継手120箇所（40d） |
| C1a | NW隅 ハンチ斜め筋 | D13 | 折曲げ | 520+780+520 | 1,820 | 6 | 10.9 | 11 | |
| C1b | NE隅 ハンチ斜め筋 | D13 | 折曲げ | 520+567+520 | 1,607 | 6 | 9.6 | 10 | |
| C2 | ハンチ縦補強筋 | D13 | L形 | 1890+300 | 2,190 | 6 | 13.1 | 13 | 各隅3本 |
| C3 | 隅角 内側横筋定着 | D13 | L形 | 延長+520 | 520 | 24 | 12.5 | 12 | 各隅6段×2面 |
| E1 | 端部コ字筋（壁） | D13 | コ形 | 520+90+520 | 1,130 | 12 | 13.6 | 13 | 2端部×6段 |
| E2 | 端部縦筋 追加 | D13 | L形 | 1890+300 | 2,190 | 4 | 8.8 | 9 | 2端部×2本 |
| R1 | 無改良補強 天端補強筋 | D19 | L形 | 6,500+760 | 7,260 | 2 | 14.5 | 33 | SD345 両面各1・継手なし |
| R2 | 無改良補強 底盤下端 壁際 | D19 | L形 | 6,500+760 | 7,260 | 3 | 21.8 | 49 | SD345 継手なし |
| R3 | 補強梁 主筋（上下各3） | D19 | L形 | 6,000+760 | 6,760 | 6 | 40.6 | 91 | SD345 継手なし |
| R4 | 補強梁 あばら筋 | D13 | 閉鎖形 | 380×840 フック135° | 2,700 | 31 | 83.7 | 83 | @200 |
| F1a | 底盤上端主筋 追加 | D13 | コ形(下向) | 300+2787+300 | 3,387 | 18 | 61.0 | 61 | F1と交互 @150 |
| F2a | 底盤下端主筋 追加 | D13 | コ形(上向) | 300+2759+300 | 3,359 | 18 | 60.5 | 60 | F2と交互 @150 |

鉄筋合計（概算・ロス別）　約 3,580 kg　≒ 3.58 t　（D13 0.995・D19 2.25・D10 0.560 kg/m）

※本数は壁延長を伸縮目地・隅角で区切った区間毎に @300 で算出（区間：西9.90 / 北5.30・15.10・5.06 / 東7.12 m）。現場で端数調整のこと。

※曲げ加工寸法は外寸。縦筋の上端は天端かぶり80で直止め。重ね継手40d(520)は千鳥配置、隅角部・目地部に継手を設けない。


## コンクリート・型枠ほか 数量（概算）

| 項目 | 数量 | 単位 | 備考 |
|---|---|---|---|
| 擁壁延長（外面） | 42.48 | m | 西9.90＋北25.46＋東7.12（改3） |
| コンクリート 底盤 t=500 | 53.07 | m³ | 底盤面積 106.1m² |
| コンクリート 立上り t=250（ハンチ含） | 17.14 | m³ | H=1,600 |
| コンクリート 計 Fc21 | 70.21 | m³ | ロス別 |
| 均しコンクリート t=50 | 5.57 | m³ | 敷地側100出し |
| 基礎砕石 t=100 | 11.15 | m³ | 転圧 |
| 型枠（外面・内面・妻） | 181 | m² | 伸縮目地妻型枠含む |
| 裏込砕石 300×800 | 9.9 | m³ | |
| 止水コンクリート 350×50 | 0.72 | m³ | |
| 面木 20×20 | 92 | m | 天端両角＋端部・出隅 |
| 目地棒 30/20×D25（誘発目地） | 22.4 | m | 7箇所×両面 |
| エラスタイト t=10（伸縮目地） | 3.8 | m² | 2箇所 |
| シーリング 10×10 | 15.9 | m | 外面・天端 |
| 前面ふかしコン W300（無筋 Fc18） | 3.27 | m³ | 北面全長＋西面1.5m |
| 前面嵩上げ盛土（転圧） | 5.5 | m³ | 平均17cm×幅約1.2m 概算 |
| 水抜穴 VP75 L=300 | 30 | 箇所 | 吸出し防止材共 |
| 補強梁（上がり梁）コンクリート Fc21 | 1.50 | m³ | 500×500 L=6.0m（S-07） |
| 補強梁 型枠 | 6.2 | m² | 両側面＋妻 |
| 【VE】ガラ割栗の水はけ層 W500×H800 | 約16 | m³ | 西・東面。透水シート共（承認後） |

## 着工前 確認事項（監督・設計者）

1. 根入れ：躯体は構造計算どおり（底盤下端 ±0-1900）。北面・西面NW側の前面地盤を ±0-1500 に嵩上げ＋前面ふかしコン W300 で根入れ400を確保。見え高さ 1,700（2m以下）。嵩上げ部は外面から1.0m以上平坦、転圧管理。
2. 天端 ±0+200 水平の可否（現況GL ±0〜+100、天端の見え高さが変わる）。
3. 西面は境界から2,929内側（北面3,000短縮）。電柱・支柱の位置を実測し新西面まで1.0m以上（推定 表面で1,904）を確認。九電と事前協議（S-06）。帯状部（旧西面位置〜新西面）の仕上げ高さ・排水・土留めを決定。
4. 外部地盤高さを実測し、水抜穴の高さ（標準／調整／省略）を確定。
5. 申請建物基礎と北面底盤（ヒール）の重なり・取合い高さ。
6. 外面型枠・足場の作業スペース（隣地承諾・道路使用）。
7. 東面（道路側）は既存地盤で根入れ790以上のため嵩上げ不要。上空線（電線）の高さを実測、重機・ポンプ車の作業高さを制限（S-06）。
8. 数量・本数は概算。鉄筋業者にて加工帳を最終チェックのこと。
9. 電線下の無改良区間（西面 NW隅から0.7〜5.0m）：打設できない改良体の範囲を改良業者と確定し、端部の改良体の再計算・増し打ちを依頼（S-07）。R1〜R4・F1a・F2a の補強は構造設計者の確認後に施工。
10. 【VE】ガラ・割栗石の場内再利用（水はけ層・埋戻し下層）は構造設計者の承認後。


形状略図

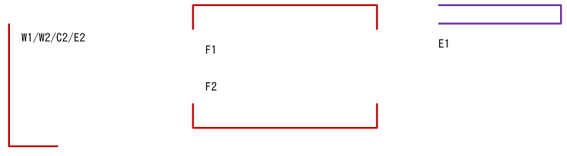


| | | | | | |
|---|---|---|---|---|---|
| 工事名<br>大信薬局様邸新築工事 | ハゼモト建設株式会社<br>一級建築士事務所<br>北九州市小倉北区片野4-12-10　TEL 093-931-0521　FAX 093-931-0927 | 管理者<br>櫨本 健一 | 設計者 | 担当者 | 図面名<br>擁壁 鉄筋加工帳・数量表 | 図面No<br>S-05 |
| 備考<br>鉄筋・型枠・土工 協力業者配布用<br>改3-2 2026/11/14 電柱側 矢板なし（S-06）・ガラ／割栗石の場内再利用（VE）／改3-1 11/11 電線下補強 | | 日付<br>2026/11/14 | 日付 | 日付 | 縮尺<br>— | 施工図 |


# 電柱回避・建柱車 施工検討図　平面 S=1/150 ／ 断面 S=1/150

## ① 平面（電柱・上空線・掘削範囲・建柱車据付候補）

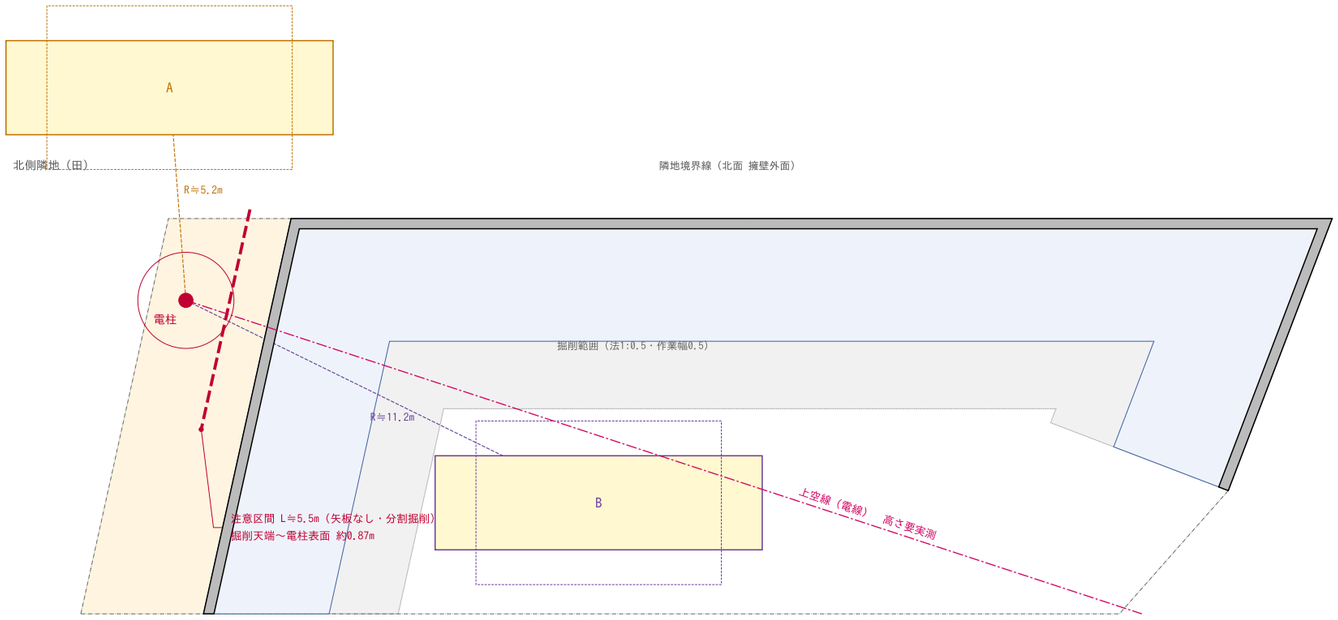


建柱車は代表寸法（全幅2.3m×全長8m、アウトリガ張出幅4m を点線）で表示。機種は九州電力の配車による。

## ② 断面（新西面に直角・電柱位置）　高さは推定・要実測

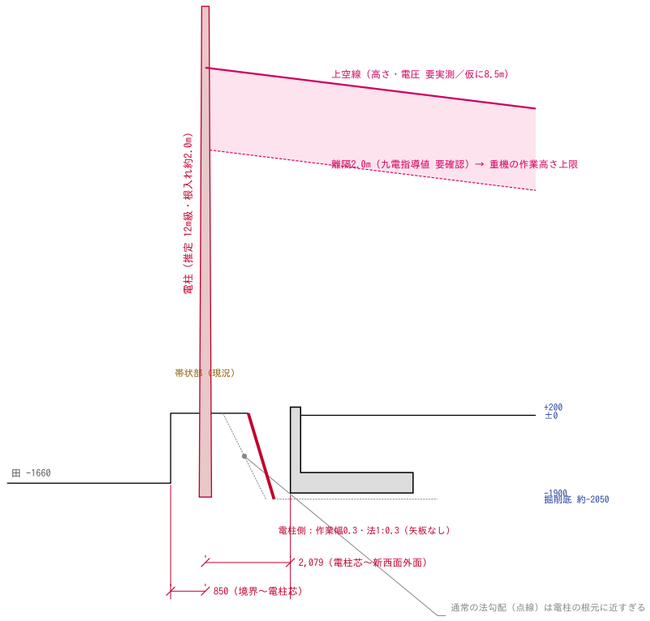


## 1. 前提（推定値・着工前に実測）

・電柱：西境界から850・北境界から2,000（配置図への手書き指示）。支柱付き。
・電柱 φ350・12m級・根入れ約2.0m と仮定。支柱の足元位置は未確認。
・上空線：電柱から南東へ敷地を斜めに横断（調査位置図）。
　電圧区分（高圧6.6kV／低圧／通信）・地上高さは未確認。

## 2. 擁壁と電柱の離れ

・新西面外面まで 芯2,079／表面1,904（必要1,000 → OK）
・通常の掘り方（作業幅0.5・法1:0.5）だと掘削天端が電柱表面から約0.25m → 不可
・方針（11/14）：矢板は使わない。電柱前後 約6mは作業幅0.3・法1:0.3で掘る
　→ 掘削天端～電柱表面 約0.87m。根入れ部に近く、十分な注意が必要。

## 3. 建柱車による電柱支持（九電作業）の可否

| 据付位置 | 電柱まで | 課題 | 判定 |
|---|---|---|---|
| A 北側隣地（田） | 約5.2m | 敷鉄板・進入路・地権者承諾 | ○ 条件付 |
| B 敷地内（掘削範囲外） | 約11m | 掘削範囲が広く遠い・上空線の下 | × 実質不可 |
| C 帯状部（旧西面～新西面） | 約2.3m幅 | 車幅＋アウトリガが入らない | × 不可 |
| D 南側道路 | 約9m以上 | 道路使用許可・作業半径大 | △ |

## 4. 上空線の下での作業（当社・協力業者）

・重機・ポンプ車・ユニック：電線から2.0m以上（九電指導値）。
　法定の最小離隔（基発第759号）：低圧1.0m／高圧1.2m。
・九電に防護管の取付を依頼。上空線の下では監視人を配置する。
・上空線の下は小旋回機（0.1～0.25m³）で作業高さを制限して使う。
・生コンはポンプ車のブームが上空線にかからない位置から打設する。


## 5. 結論・【警告】電柱側の掘削（矢板なし）

①電柱前後 約6mは長さ2m程度ずつ分割して掘り、当日中に砕石・捨てコンまで進める。
②掘削中は九電の立会い。電柱の傾きを下げ振り・トランシットで朝・昼・夕に確認。
③雨天・雨の翌日は電柱側を掘らない。法面はシートで養生する。
④電柱周り1.0mに重機・ダンプ・資材を置かない。支柱の足元も同様。
⑤傾き・亀裂・湧水が出たら直ちに掘削を止めて埋め戻し、九電と協議する。
⑥九電が支持を求めた場合は、北側隣地（A）に建柱車を据えて支持する。
⑦柱状改良機は電線下に入れない → 西面 NW隅から0.7～5.0mは無改良とし底盤補強（S-07）。
⑧着工前に九電と現地立会い：電柱・支柱・電線の位置と高さ、
　支持の要否、防護管、作業日程、費用負担を確認する。


| | | | | | |
|---|---|---|---|---|---|
| 工事名<br>大信薬局様邸新築工事 | ハゼモト建設株式会社<br>一級建築士事務所<br>北九州市小倉北区片野4-12-10　TEL 093-931-0521　FAX 093-931-0927 | 管理者<br>櫨本 健一 | 設計者 | 担当者 | 図面名<br>電柱回避・建柱車 施工検討図 | 図面No<br>S-06 |
| 備考<br>鉄筋・型枠・土工 協力業者配布用<br>改3-2 2026/11/14 電柱側 矢板なし（S-06）・ガラ／割栗石の場内再利用（VE）／改3-1 11/11 電線下補強 | | 日付<br>2026/11/14 | 日付 | 日付 | 縮尺<br>1/150 | 施工図 |

# 電線下 無改良区間（柱状改良なし）底盤補強図・配筋図


## ① 平面（西面 NW隅付近） S=1/50

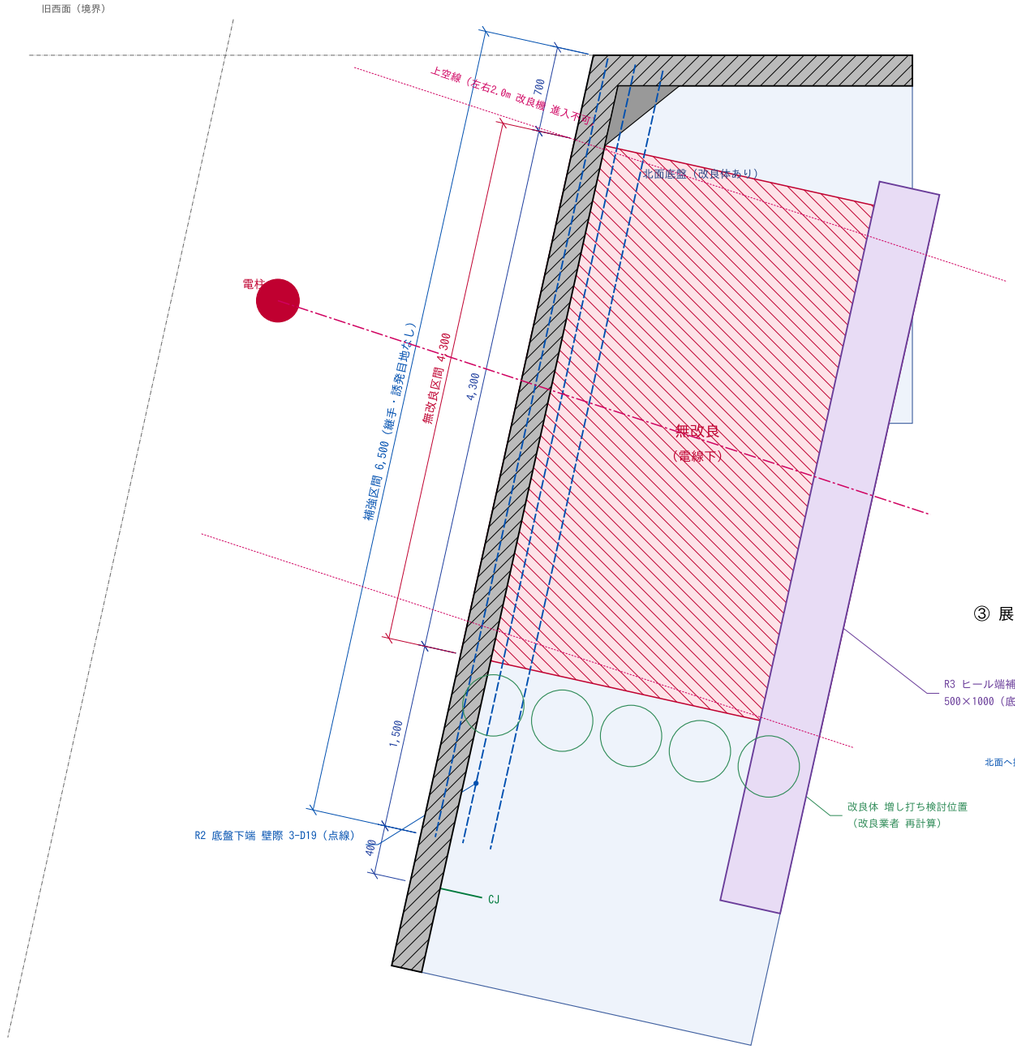


## ② 断面 B-B（無改良区間・補強区間共通） S=1/30

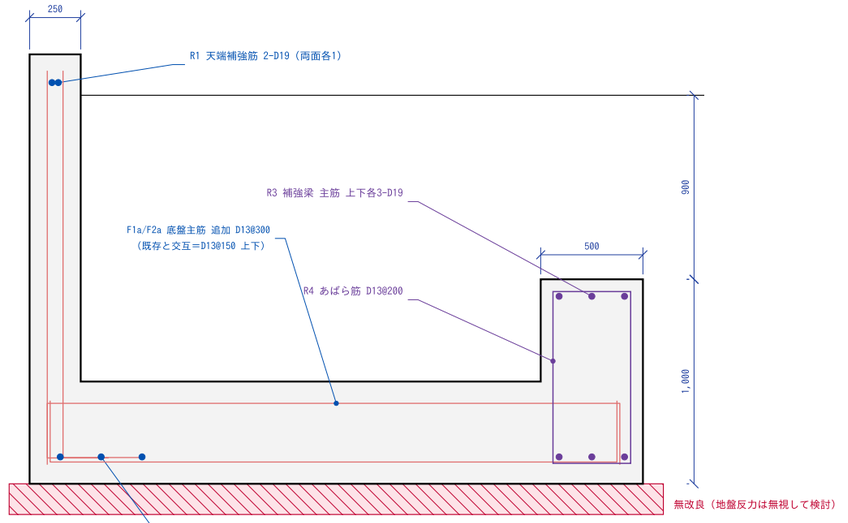


## ③ 展開（敷地内側より・西面 NW隅～） S=1/50

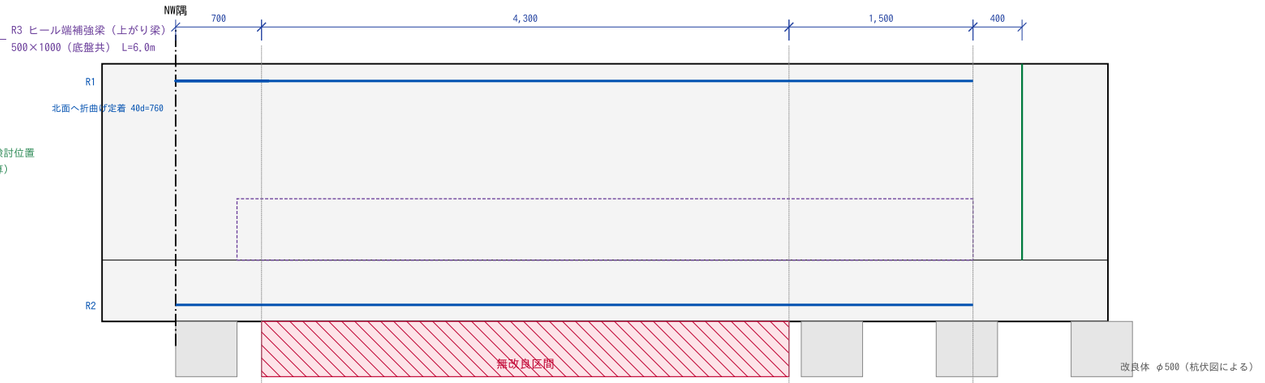


## ④ 補強検討（長期・許容応力度。無改良区間の地盤反力は無視）

| 項目 | 立上り＋底盤（L形断面） | ヒール端補強梁 | ヒール版（横方向） |
|---|---|---|---|
| 荷重 w（kN/m） | 68.7 | 75.2 | q=47.2 kN/m² |
| スパン L（m） | 4.80 | 3.09 | 2.625 |
| M=wL²/8（kN·m） | 198 | 90 | 40.7/m |
| 有効せい d（mm） | 1990 | 877 | 393 |
| 必要At（mm²） | 528 | 545 | 606/m |
| 配筋（引張側） | 下端3-D19＋2-D13／天端2-D19＋2-D13 | 上下各3-D19 | D13@150 上下 |
| 許容 Ma（kN·m） | 301 | 142 | 56.7/m |
| せん断 τ（N/mm²）≦0.70 | 0.38 | 0.30 | — |
| 判定 | OK | OK | OK |

荷重：立上り・底盤 γc=24、ヒール上の土 1.4m×γ18、積載10kN/m²。全断面 143.9kN/m を立上り側と補強梁側に配分。

許容応力度：SD345（D19）215、SD295（D13）195、Fc21 長期せん断 0.70 N/mm²。j=7/8d。端部は単純支持として安全側に評価。

支点反力：南端・隅角側とも約281kN → 隣接する改良体へ集中。改良体の再計算・増し打ちを改良業者に依頼。

## ⑤ 特記事項

1. 無改良区間：西面 NW隅から 700～5,000（底盤全幅）。
   電線の平面位置から左右2.0mは改良機が入れない（推定）。
   打設できない改良体の範囲は改良業者と現地で確定する。
2. 補強区間：NW隅～6,500（無改良区間の両側へ1,500以上）。
   区間内は補強筋・横筋とも継手禁止、誘発目地なし
   （西面のCJは 6,900 の1か所に変更）。
3. R1・R2 は北端を北面へ折曲げ定着（40d=760）、
   南端は無改良区間端から1.5m以上延ばし直止め。
4. R3 補強梁は北面底盤（改良体あり）に一体打設で定着。
5. 底盤主筋 F1・F2 は補強区間で D13@150（追加 F1a・F2a）。
6. 無改良区間の底盤下も基礎砕石t100＋均しコンt50。
7. 本補強は概略検討。構造設計者の確認後に施工する。
8. 補強梁部の掘削・打設は電線下の作業高さ制限による（S-06）。

| | | | | | | |
|---|---|---|---|---|---|---|
| 工事名<br>大信薬局様邸新築工事 | ハゼモト建設株式会社<br>一級建築士事務所<br>北九州市小倉北区片野4-12-10 TEL 093-931-0521 FAX 093-931-0927 | 管理者<br>檜本 健一 | 設計者 | 担当者 | 図面名<br>電線下 無改良区間 底盤補強図 | 図面No<br>S-07 |
| 備考<br>鉄筋・型枠・土工 協力業者配布用<br>改3-2 2026/11/14 電柱側 矢板なし（S-06）・ガラ／割栗石の場内再利用（VE）／改3-1 11/11 電線下補強 | | 日付<br>2026/11/14 | 日付 | 日付 | 縮尺<br>1/50・1/30 | 施工図 |