
擁壁 平面割付図　S=1/100

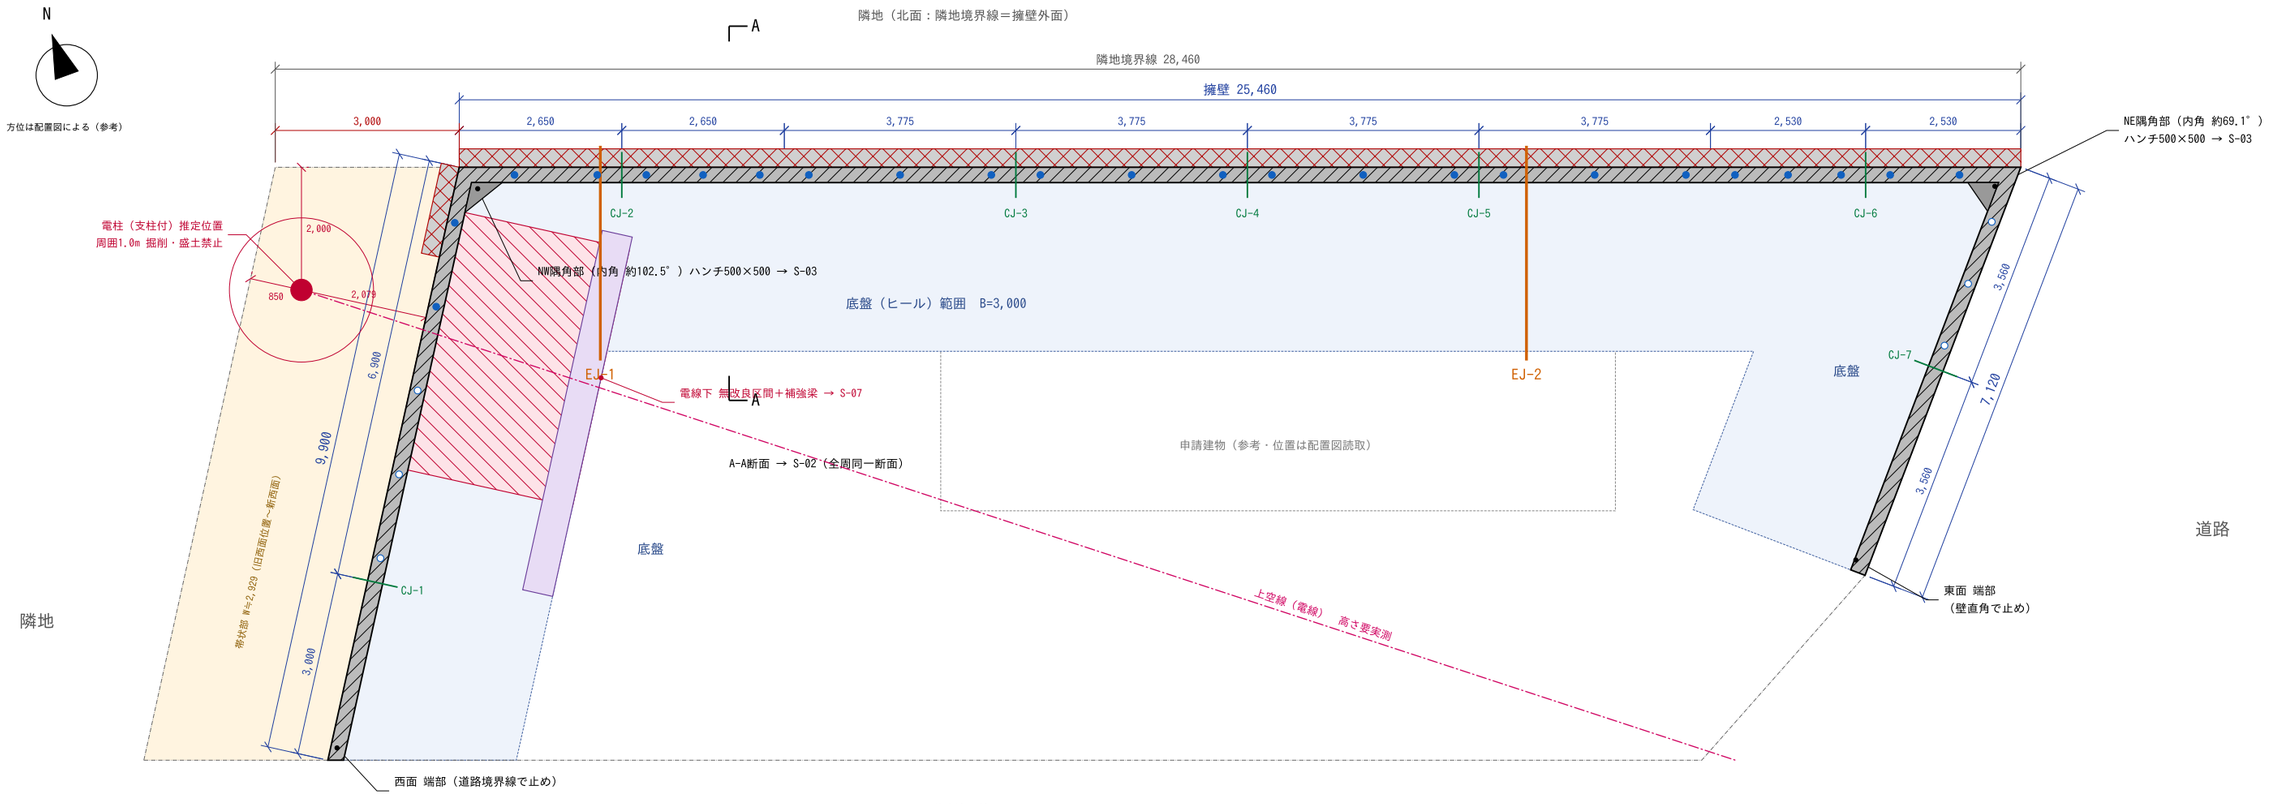

目地・水抜穴 割付表（寸法は擁壁外面＝境界線に沿う）

面	延長	誘発目地 CJ 位置	伸縮目地 EJ 位置	水抜穴
西面	9,900	NW隅から 6,900	—	5 箇所
北面	25,460	NW隅から 2,650 / 9,075 / 12,850 / 16,625 / 22,930	NW隅から 5,300 / 20,400	22 箇所
東面	7,120	NE隅から 3,560	—	3 箇所
計	42,480	7 箇所	2 箇所	30 箇所

水抜穴 位置表（隅角部からの距離 / 芯高さ ±0基準）

西面（NW隅→南）：　900 / 2,300 / 3,700[-950] / 5,100[-750] / 6,500[-550] / 7,300(省略) / 8,400(省略) / 9,500(省略)

北面（NW隅→東）：　900 / 2,250 / 3,050 / 3,975 / 4,900 / 5,700 / 7,188 / 8,675 / 9,475 / 10,963 / 12,450 / 13,250 / 14,738 / 16,225 / 17,025
18,512 / 20,000 / 20,800 / 21,665 / 22,530 / 23,330 / 24,460

東面（NE隅→南）：　1,000[-800] / 2,080[-650] / 3,160[-500] / 3,960(省略) / 5,340(省略) / 6,720(省略)

※無印＝標準高さ GL-1060（止水コン天端に管底）。[ ]内＝調整高さ（外部地盤+150）。(省略)＝外部地盤が高く排水不可のため設けない。
※外部地盤は配置図からの読取値。墨出し時に外部地盤高さを実測し、右記ルールで最終高さを決定すること。

凡例


- 立上り t=250
- 底盤 B3000 t500
- EJ 伸縮目地
- CJ 誘発目地
- 水抜穴 標準高さ
- 水抜穴 高さ調整
- 前面ふかしコン

特記事項

1. 北面・東面の擁壁外面＝隣地／道路境界線。西面は境界から敷地側へ
   北面に沿って 3,000 移動（境界と平行、直角離れ 2,929）。NW隅＝新隅角。
2. 壁角度は配置図読取値（NW隅 約102.5° ・NE隅 約69.1°）。
   境界杭にて現地確認のうえ墨出しすること。
3. 伸縮目地 EJ：全断面（立上り＋底盤）縁切り、
   区間長 15.2m／15.1m／12.2m（≦20m）、隅角部から2m以上離す。
4. 誘発目地 CJ：立上り両面に目地棒、間隔 4.1m以内。
5. 水抜穴：VP75（内径75以上）、1.5m以内ピッチ
   （露出面 約1.9m²/箇所 ≦3m²）、外部へ2%以上の勾配。
   高さルール：外部地盤 ≦GL-1210 → GL-1060(標準)
   GL-1210～-650 → 外部地盤+150
   GL-650 超 → 設けない
6. 隅角部（2箇所）はハンチ500×500＋補強筋（S-03）。
7. 断面・配筋は S-02、目地・隅角・端部詳細は S-03、
   展開図は S-04、鉄筋加工帳・数量は S-05 による。
8. 根入れ：北面全長・西面NW隅から1.5mは前面地盤を ±0-1500 に
   嵩上げ＋前面ふかしコン W300（無筋）で根入れ400を確保。
9. 電柱（推定位置）：西境界から850・北境界から2,000。新西面外面まで
   芯で約2,079（表面で約1,904≧1,000）。電柱・支柱の位置は
   着工前に実測。周囲1.0mは掘削・盛土禁止。施工検討は S-06。
10. 電線下で柱状改良を打てない区間（西面 NW隅から700～5,000）は
    底盤補強＋ヒール端補強梁で両側の改良区間へ架け渡す（S-07）。
11. 【VE・改3-2】解体ガラ（土間コン・ブロック）と割栗石は処分せず場内で再利用。
    裏込め砕石の外側の水はけ層（S-02）・西／東面ヒール上の埋戻し下層・帯状部・
    北側嵩上げの下層。北面ヒール上（建物の下）には使わない。構造設計者の承認後。

工事名 大信薬局様邸新築工事	ハゼモト建設株式会社 一級建築士事務所 北九州市小倉北区片野4-12-10　TEL 093-931-0521　FAX 093-931-0927	管理者 檜本 健一	設計者	担当者	図面名 擁壁 平面割付図	図面No S-01
備考 鉄筋・型枠・土工 協力業者配布用 改3-2 2026/11/14 電柱側 矢板なし（S-06）・ガラ／割栗石の場内再利用（VE）／改3-1 11/11 電線下補強		日付 2026/11/14	日付	日付	縮尺 1/100	施工図

擁壁 標準断面配筋図（A-A 全周共通）　S=1/20

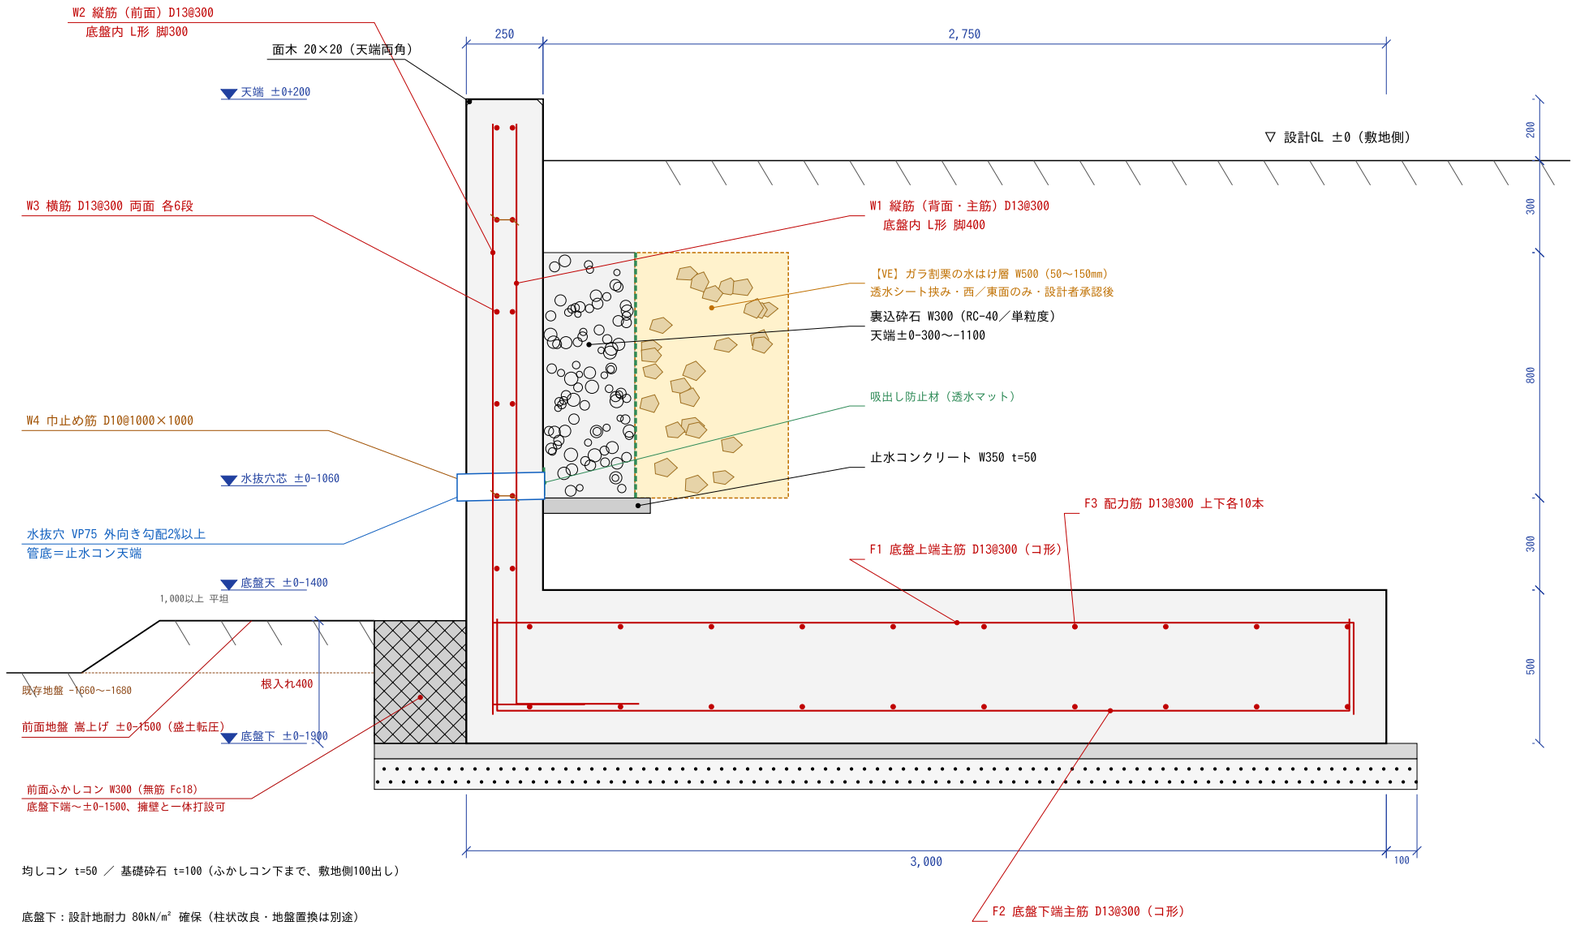

均しコン t=50 ／ 基礎砕石 t=100（ふかしコン下まで、敷地側100出し）


底盤下：設計地耐力 80kN/m² 確保（柱状改良・地盤置換は別途）

設計条件・配筋特記


設計地耐力 80kN/m²　地表面積載荷重 10kN/m²
コンクリート Fc=21N/mm²（呼び強度は構造体補正 mSn を加算）
鉄筋 SD295　かぶり厚さ：壁 80 ／ 底盤 100（全面）
重ね継手 40d（D13＝520）千鳥継手　定着 35d（フック付 25d）
スペーサー：壁 80用 縦横@1,000以内／底盤 サイコロ100 @1,000以内
打継ぎ：底盤天で水平打継ぎ。レイタンス除去・目荒らし後に立上り打設。
縦筋は先組し底盤と同時に固定、打設時に移動させないこと。
縦筋は前面・背面とも 外側、横筋は内側に配筋（有効せい確保）。

部分詳細　S=1/10

① 天端（面木）

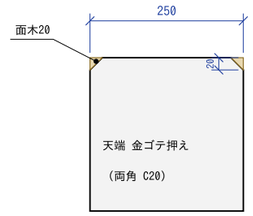


② 誘発目地 CJ（平面）

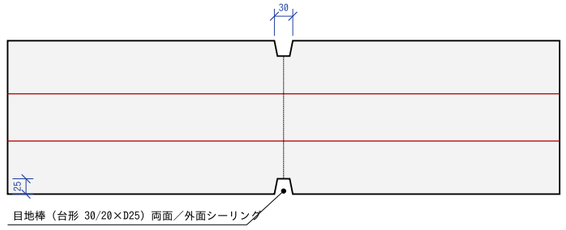

断面欠損 50/250＝20%　横筋は連続
範囲：天端～底盤天（立上り部のみ）

③ 水抜穴（断面）

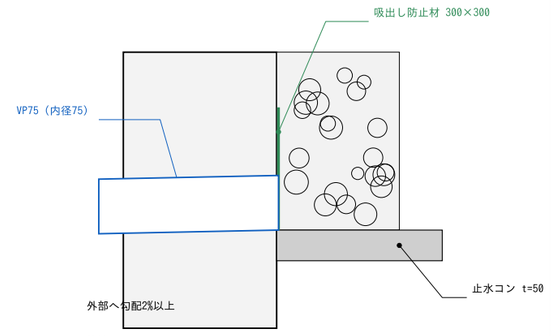

工事名 大信薬局様邸新築工事	ハゼモト建設株式会社 一級建築士事務所 北九州市小倉北区片野4-12-10　TEL 093-931-0521　FAX 093-931-0927	管理者 檜本 健一	設計者	担当者	図面名 擁壁 標準断面配筋図	図面No S-02
備考 鉄筋・型枠・土工 協力業者配布用 改3-2 2026/11/14 電柱側 矢板なし（S-06）・ガラ／割栗石の場内再利用（VE）／改3-1 11/11 電線下補強		日付 2026/11/14	日付	日付	縮尺 1/20・1/10	施工図