
擁壁詳細図　1/30

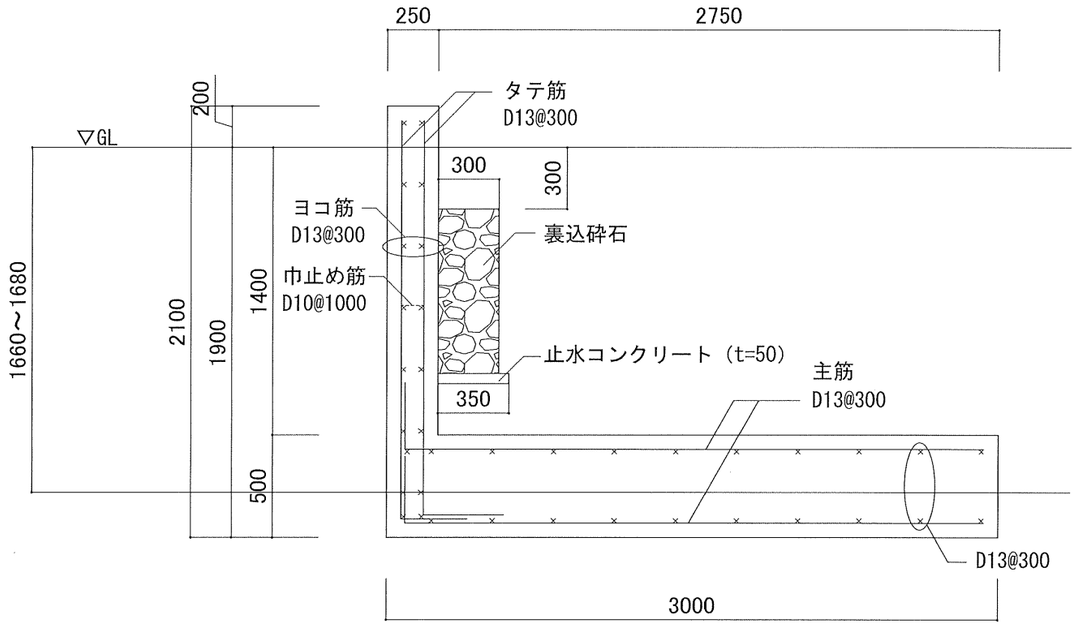

設計条件

設計地耐力：80KN/㎡
地表面積載荷重：10KN/㎡
コンクリート設計基準強度：21KN/㎥
鉄筋：SD295
鉄筋の被り厚さ：壁8cm　底盤10cm

※水抜き孔は内径7.5cm以上とする。
※水抜き孔は壁面3㎡ごとに設けること。
※水抜き孔の周辺は透水層を設けること。

工事名 大信薬局様邸新築工事	ハゼモト建設株式会社 一級建築士事務所 一級建築士第226728号 櫨本 健一	管理者	設計者	担当者	図面名 擁壁詳細図	図面ＮＯ
備考 備考は未入力	北九州市小倉北区片野4-12-10 TEL 093-931-0521 FAX 093-931-0927	日付 フリーは未入力	日付 フリーは未入力	日付 2026/08/11	縮尺 1/30	