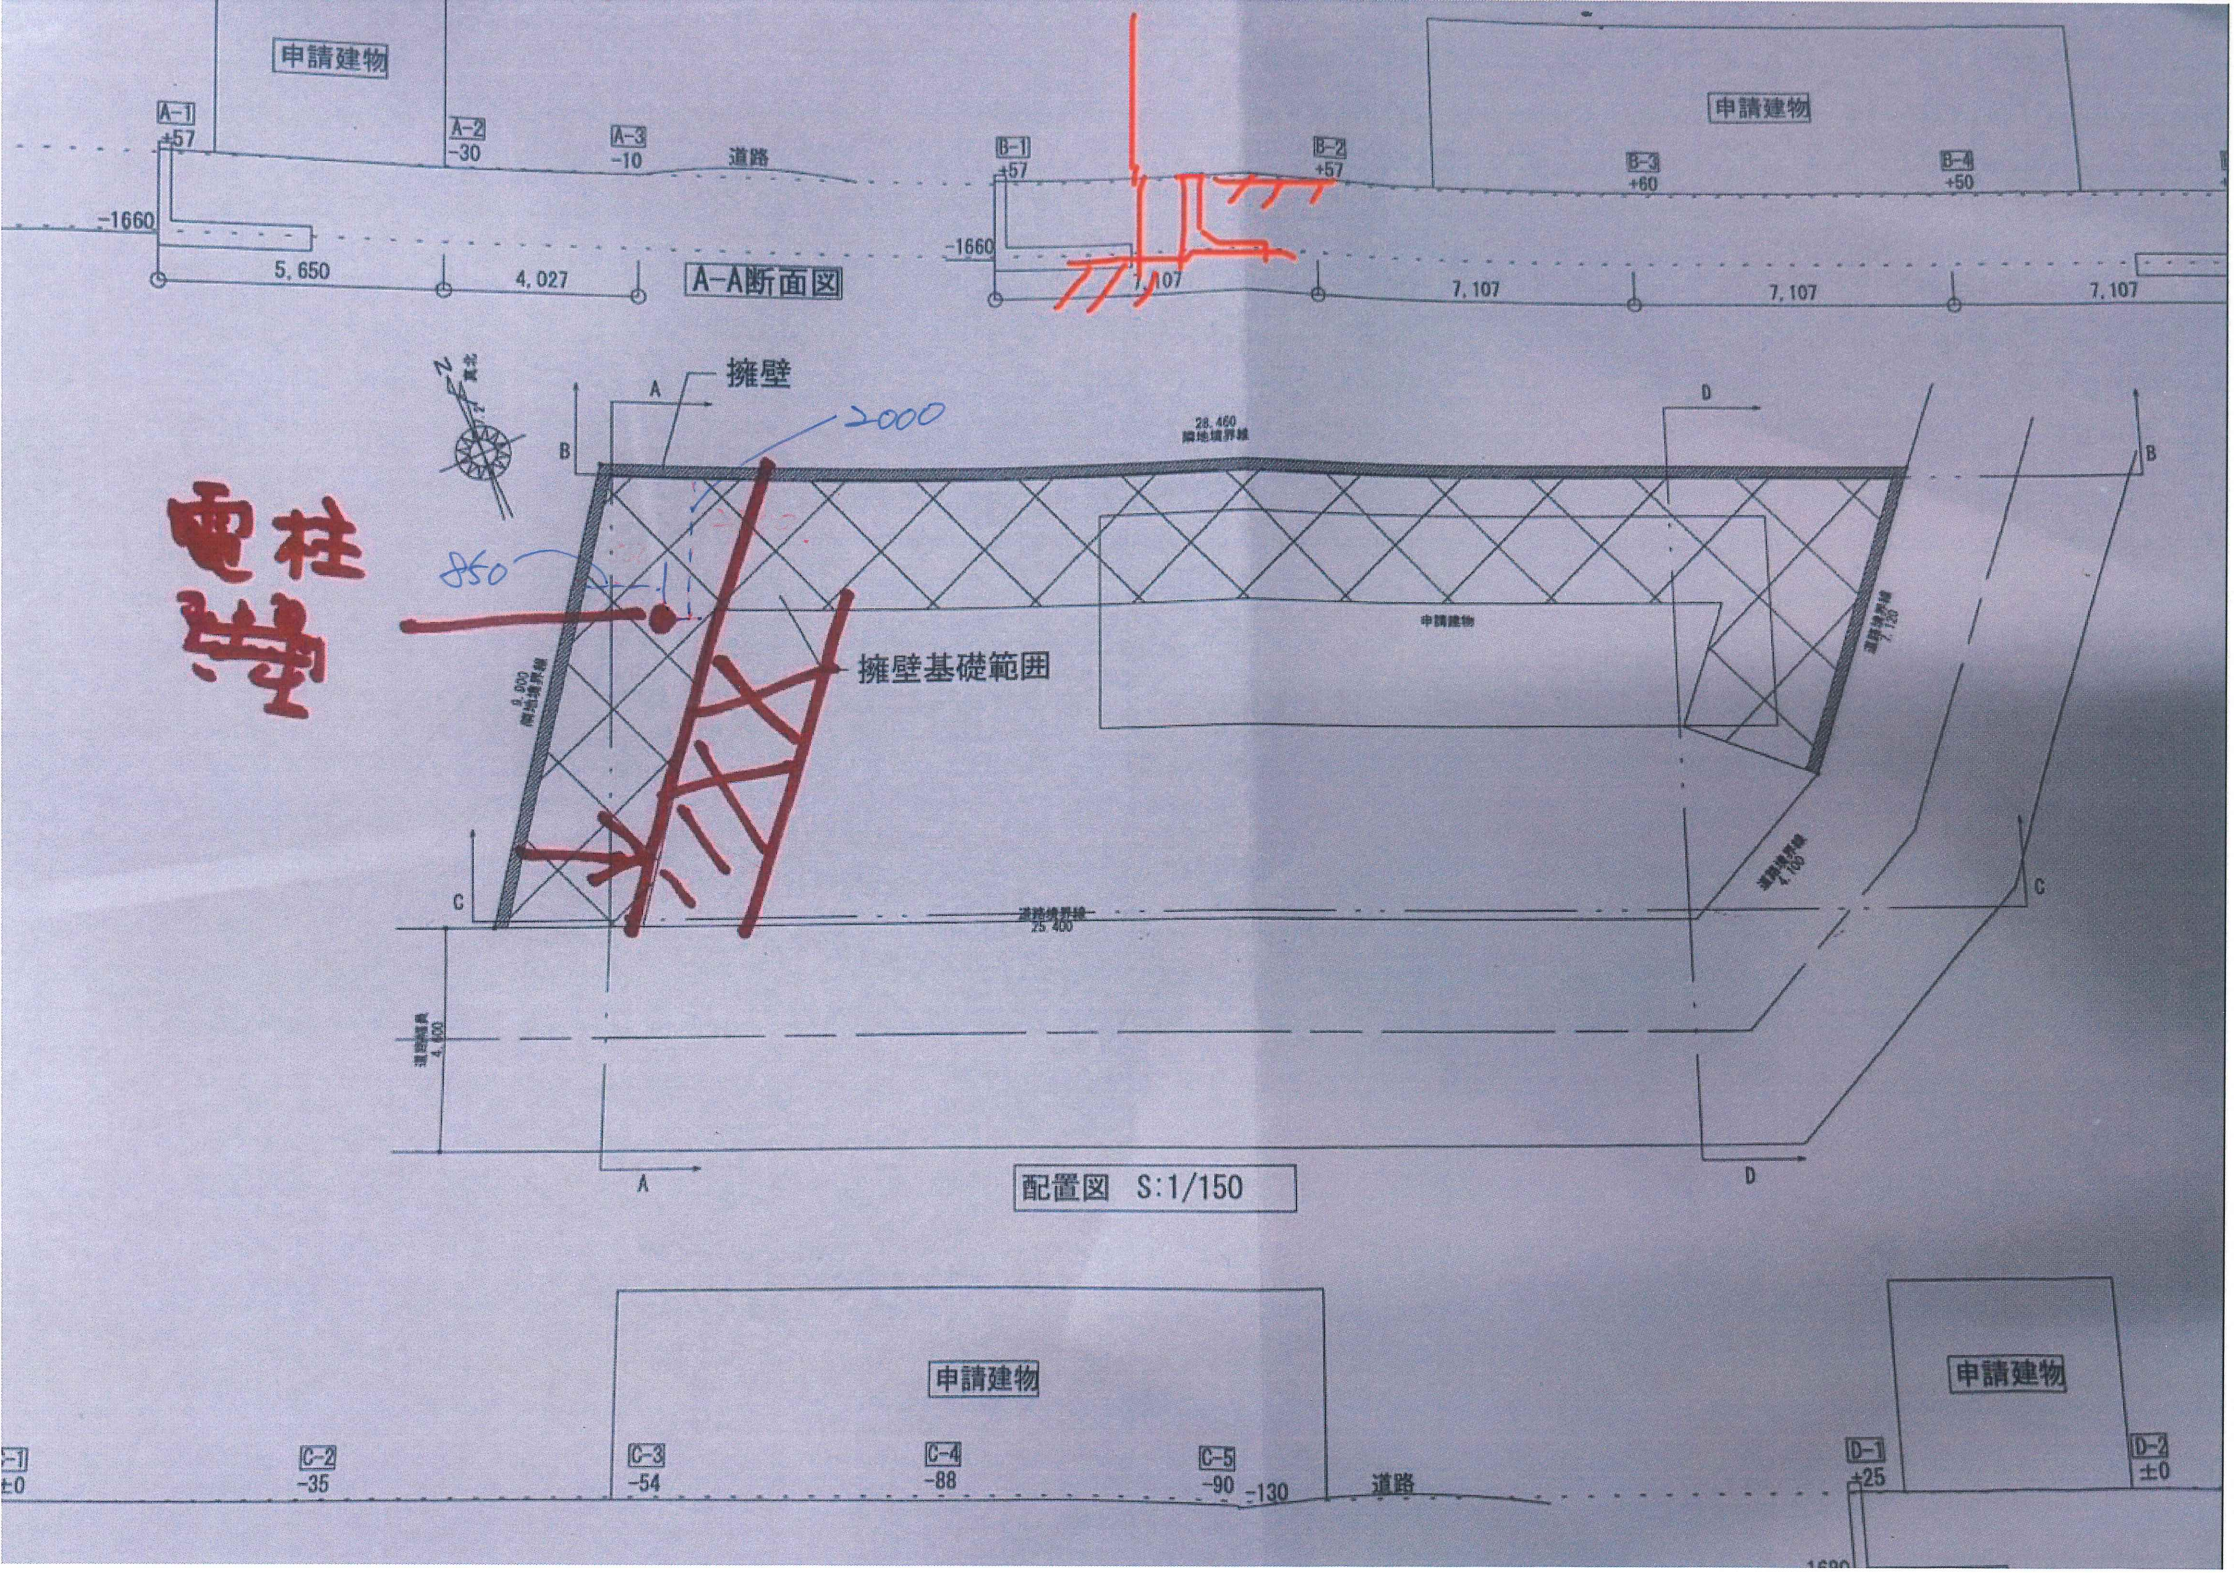

申請建物
A-1
±57
A-2
-30
A-3
-10
道路
-1660
5,650
4,027
A-A断面図
申請建物
B-1
±57
B-2
+57
B-3
+60
B-4
+50
-1660
7,107
7,107
7,107
7,107
擁壁
2000
850
擁壁基礎範囲
電柱
28,460
隣地境界線
申請建物
8,000
隣地境界線
道路境界線
25,400
道路境界線
4,100
道路境界線
7,250
道路境界線
4,100
A
B
C
D
配置図 S:1/150
申請建物
申請建物
C-1
±0
C-2
-35
C-3
-54
C-4
-88
C-5
-90
-130
道路
D-1
±25
D-2
±0