
擁壁 平面割付図　S=1/100

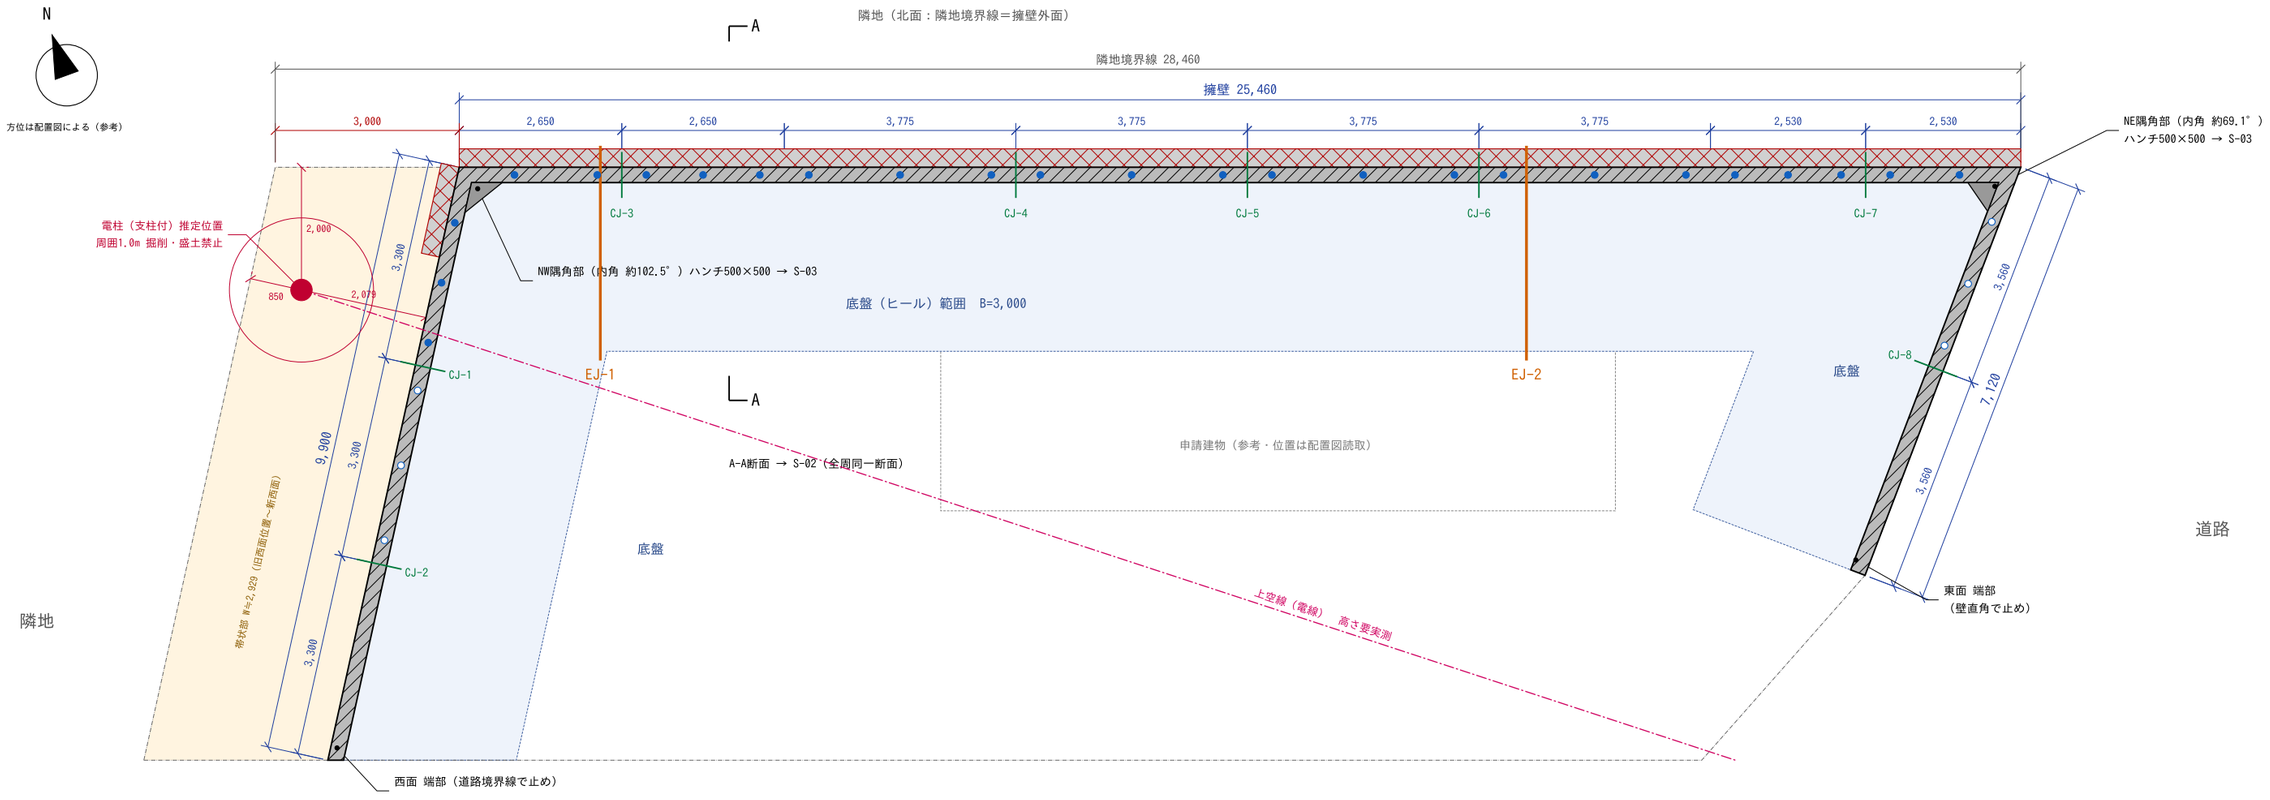

目地・水抜穴 割付表（寸法は擁壁外面＝境界線に沿う）

面	延長	誘発目地 CJ 位置	伸縮目地 EJ 位置	水抜穴
西面	9,900	NW隅から 3,300 / 6,600	—	6 箇所
北面	25,460	NW隅から 2,650 / 9,075 / 12,850 / 16,625 / 22,930	NW隅から 5,300 / 20,400	22 箇所
東面	7,120	NE隅から 3,560	—	3 箇所
計	42,480	8 箇所	2 箇所	31 箇所

水抜穴 位置表（隅角部からの距離 / 芯高さ ±0基準）

西面（NW隅→南）：　900 / 1,900 / 2,900 / 3,700[−950] / 4,950[−750] / 6,200[−600] / 7,000(省略) / 8,250(省略) / 9,500(省略)

北面（NW隅→東）：　900 / 2,250 / 3,050 / 3,975 / 4,900 / 5,700 / 7,188 / 8,675 / 9,475 / 10,963 / 12,450 / 13,250 / 14,738 / 16,225 / 17,025
18,512 / 20,000 / 20,800 / 21,665 / 22,530 / 23,330 / 24,460

東面（NE隅→南）：　1,000[−800] / 2,080[−650] / 3,160[−500] / 3,960(省略) / 5,340(省略) / 6,720(省略)

※無印＝標準高さ GL−1060（止水コン天端に管底）。[ ]内＝調整高さ（外部地盤+150）。(省略)＝外部地盤が高く排水不可のため設けない。
※外部地盤は配置図からの読取値。墨出し時に外部地盤高さを実測し、右記ルールで最終高さを決定すること。

凡例


- 立上り t=250
- 底盤 B3000 t500
- EJ 伸縮目地
- CJ 誘発目地
- 水抜穴 標準高さ
- 水抜穴 高さ調整
- 前面ふかしコン

特記事項

1. 北面・東面の擁壁外面＝隣地／道路境界線。西面は境界から敷地側へ
   北面に沿って 3,000 移動（境界と平行、直角離れ 2,929）。NW隅＝新隅角。
2. 壁角度は配置図読取値（NW隅 約102.5° ・NE隅 約69.1°）。
   境界杭にて現地確認のうえ墨出しすること。
3. 伸縮目地 EJ：全断面（立上り＋底盤）縁切り、
   区間長 15.2m／15.1m／12.2m（≦20m）、隅角部から2m以上離す。
4. 誘発目地 CJ：立上り両面に目地棒、間隔 4.1m以内。
5. 水抜穴：VP75（内径75以上）、1.5m以内ピッチ
   （露出面 約1.9m²/箇所 ≦3m²）、外部へ2%以上の勾配。
   高さルール：外部地盤 ≦GL−1210 → GL−1060(標準)
   GL−1210～−650 → 外部地盤+150
   GL−650 超 → 設けない
6. 隅角部（2箇所）はハンチ500×500＋補強筋（S-03）。
7. 断面・配筋は S-02、目地・隅角・端部詳細は S-03、
   展開図は S-04、鉄筋加工帳・数量は S-05 による。
8. 根入れ：北面全長・西面NW隅から1.5mは前面地盤を ±0−1500 に
   嵩上げ＋前面ふかしコン W300（無筋）で根入れ400を確保。
9. 電柱（推定位置）：西境界から850・北境界から2,000。新西面外面まで
   芯で約2,079（表面で約1,904≧1,000）。電柱・支柱の位置は
   着工前に実測。周囲1.0mは掘削・盛土禁止。施工検討は S-06。

工事名 大信薬局様邸新築工事	ハゼモト建設株式会社 一級建築士事務所 北九州市小倉北区片野4-12-10　TEL 093-931-0521　FAX 093-931-0927	管理者 檜本 健一	設計者	担当者	図面名 擁壁 平面割付図	図面No S-01
備考 鉄筋・型枠・土工 協力業者配布用 改3 2026/11/05 電柱回避：西面を3.0m敷地側へ移動（北面3.0m短縮）／断面は構造計算どおり		日付 2026/11/05	日付	日付	縮尺 1/100	施工図

擁壁 標準断面配筋図（A-A 全周共通）　S=1/20

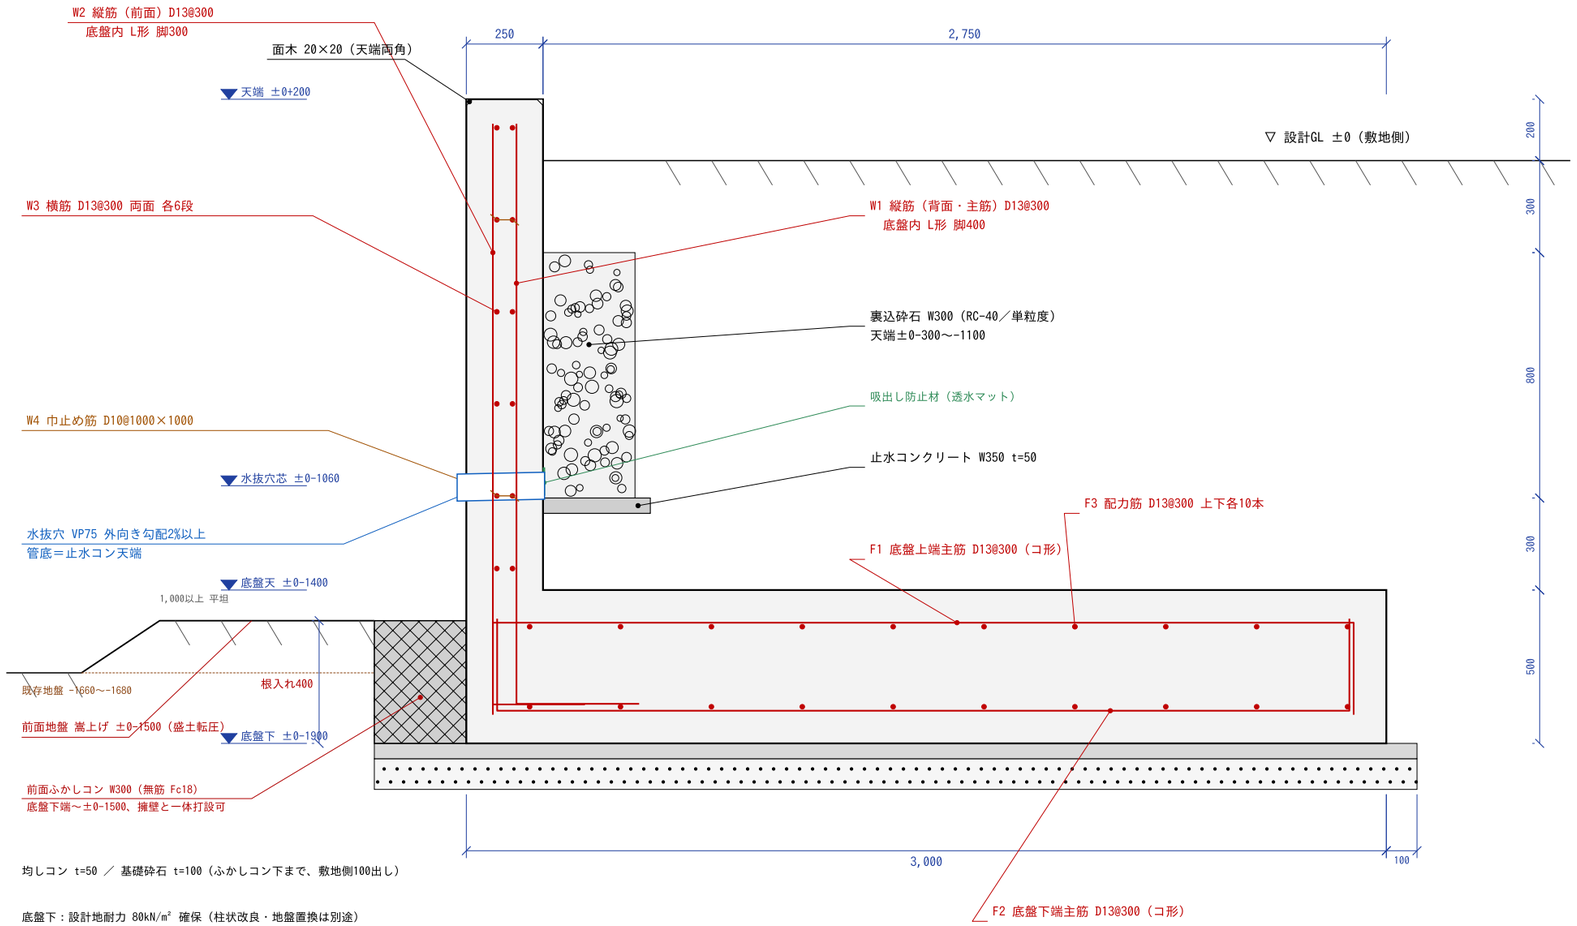

均しコン t=50 ／ 基礎砕石 t=100（ふかしコン下まで、敷地側100出し）


底盤下：設計地耐力 80kN/m² 確保（柱状改良・地盤置換は別途）

設計条件・配筋特記


設計地耐力 80kN/m²　地表面積載荷重 10kN/m²
コンクリート Fc=21N/mm²（呼び強度は構造体補正 mSn を加算）
鉄筋 SD295　かぶり厚さ：壁 80 ／ 底盤 100（全面）
重ね継手 40d（D13＝520）千鳥継手　定着 35d（フック付 25d）
スペーサー：壁 80用 縦横@1,000以内／底盤 サイコロ100 @1,000以内
打継ぎ：底盤天で水平打継ぎ。レイタンス除去・目荒らし後に立上り打設。
縦筋は先組し底盤と同時に固定、打設時に移動させないこと。
縦筋は前面・背面とも 外側、横筋は内側に配筋（有効せい確保）。

部分詳細　S=1/10

① 天端（面木）

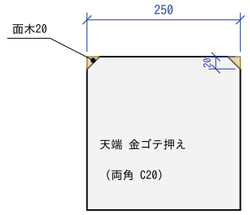


② 誘発目地 CJ（平面）

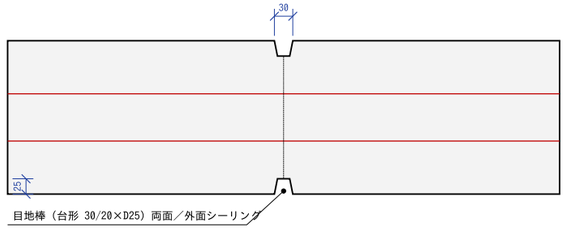

断面欠損 50/250＝20%　横筋は連続
範囲：天端～底盤天（立上り部のみ）


③ 水抜穴（断面）

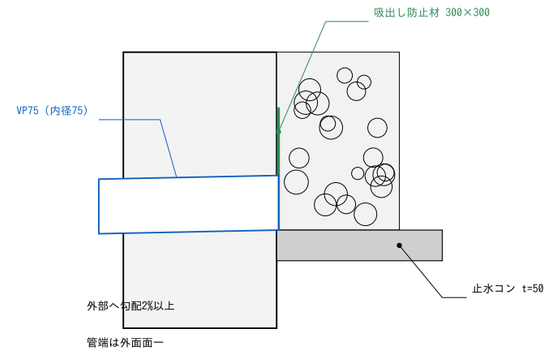

工事名 大信薬局様邸新築工事	ハゼモト建設株式会社 一級建築士事務所 北九州市小倉北区片野4-12-10　TEL 093-931-0521　FAX 093-931-0927	管理者 櫨本 健一	設計者	担当者	図面名 擁壁 標準断面配筋図	図面No S-02 施工図
備考 鉄筋・型枠・土工 協力業者配布用 改3 2026/11/05 電柱回避：西面を3.0m敷地側へ移動（北面3.0m短縮）／断面は構造計算どおり		日付 2026/11/05	日付	日付	縮尺 1/20・1/10	


伸縮目地・誘発目地・隅角部・端部 詳細

① 伸縮目地 EJ（平面） S=1/10

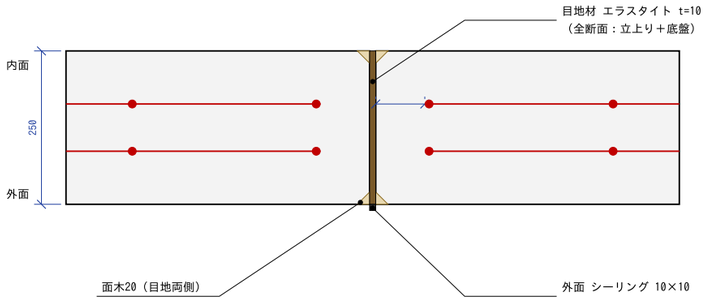


・鉄筋は目地で切断（目地面かぶり 壁80／底盤100）
・底盤も同位置で縁切り。妻型枠を立て片側ずつ打設
・天端・外面の目地際は面木20で面取り
・位置：北面 NW隅から 5,300 ／ 20,400（S-01）
・改3：NW隅＝新西面と北面の交点（境界NW角から東へ3,000）

② 誘発目地 CJ（立面・外面） S=1/30

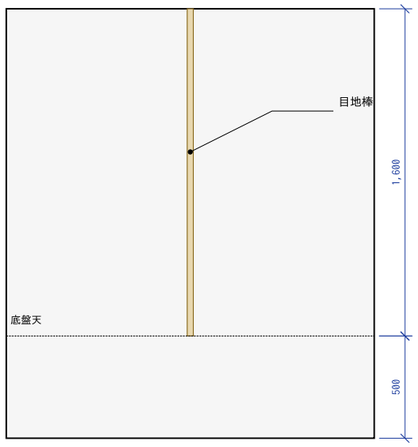


・目地棒 台形 30/20×D25（木製又は樹脂製）
　立上り 両面、天端～底盤天まで通す
・天端は目地位置で V カット 10
・断面欠損 50/250＝20%、横筋は連続
・外面側目地にシーリング 10×10
・底盤部は連続（目地を設けない）

③ NW隅角部（平面） S=1/30　内角 約102.5°

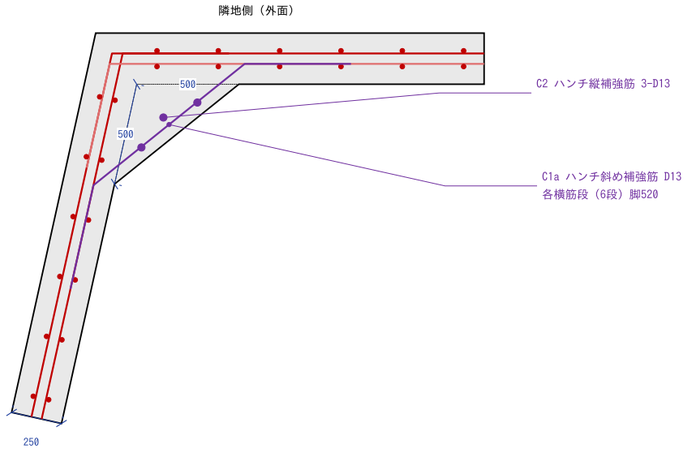


【隅角部 共通】
・外面側横筋：隅角部で折曲げ連続（継手を設けない。やむを得ない場合は重ね520）
・内面側横筋：相手壁の外面側横筋位置まで延ばし、折曲げて 520 定着（C3）
・ハンチ：二等辺三角形 500×500（宅地防災マニュアル H≦3m）、天端～底盤天まで全高
・底盤：隅角部は両方向の主筋・配力筋を重ねて配置し一体打設
・伸縮目地・誘発目地は隅角部から2m以上離す（S-01割付済）
・NE隅は鋭角（約69°）：出隅に面木20、鋭角部のかぶり80を必ず確保

⑤ 壁端部（平面） S=1/20

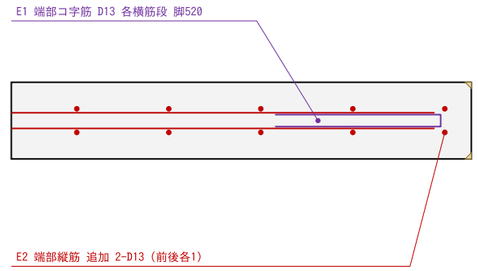


・西面端部：道路境界線に沿って止め
・東面端部：壁に直角に止め
・端部の鉛直出隅は面木20
・底盤端部は配力筋を90°フック（余長300）


④ NE隅角部（平面） S=1/30　内角 約69.1°

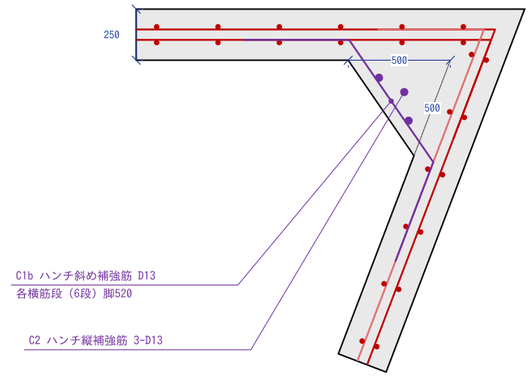

工事名 大信薬局様邸新築工事	ハゼモト建設株式会社 一級建築士事務所 北九州市小倉北区片野4-12-10 TEL 093-931-0521 FAX 093-931-0927	管理者 櫨本 健一	設計者	担当者	図面名 擁壁 目地・隅角部・端部詳細	図面No S-03
備考 鉄筋・型枠・土工 協力業者配布用 改3 2026/11/05 電柱回避：西面を3.0m敷地側へ移動（北面3.0m短縮）／断面は構造計算どおり		日付 2026/11/05	日付	日付	縮尺 1/10・1/20・1/30	施工図

擁壁 展開図（敷地内側より見る）　S=1/60　※水抜穴は外面まで貫通

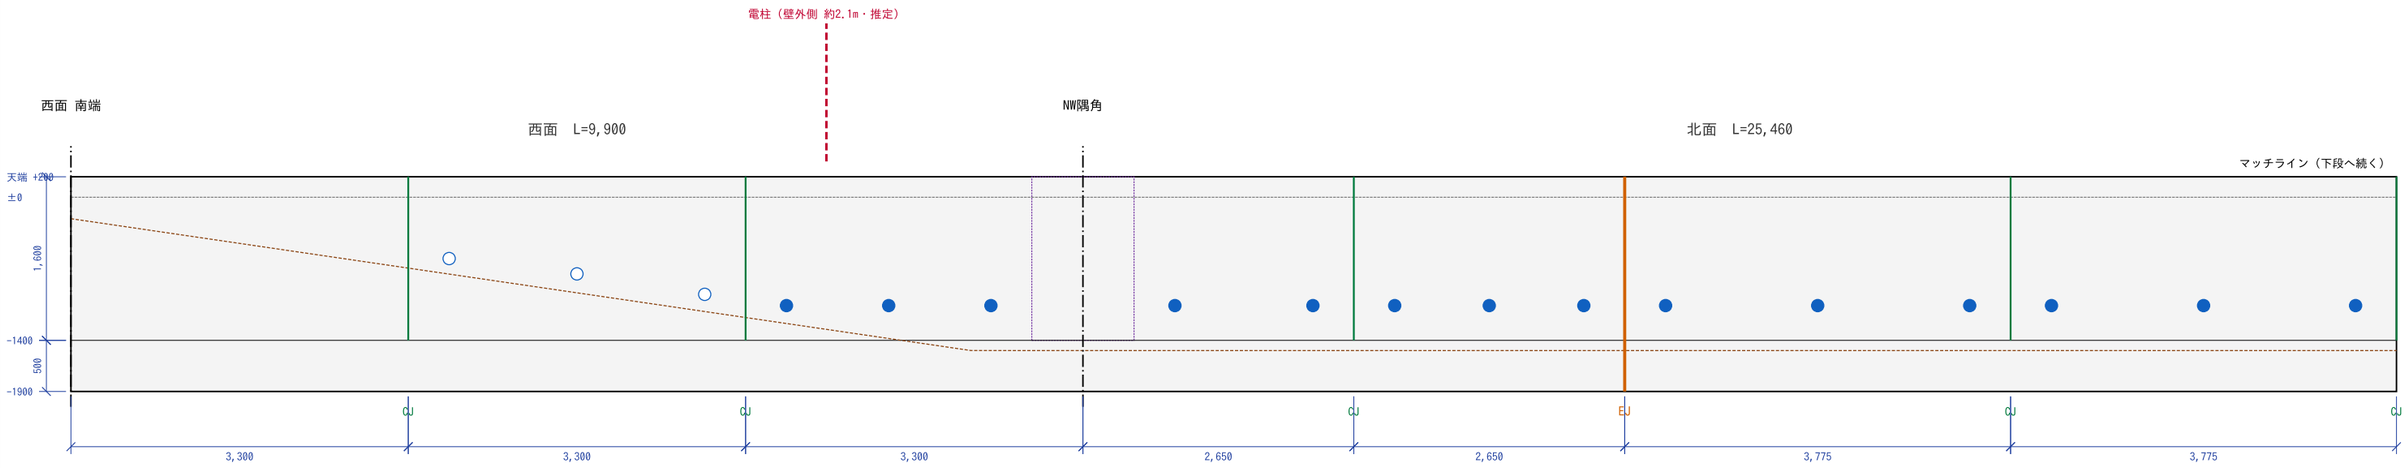

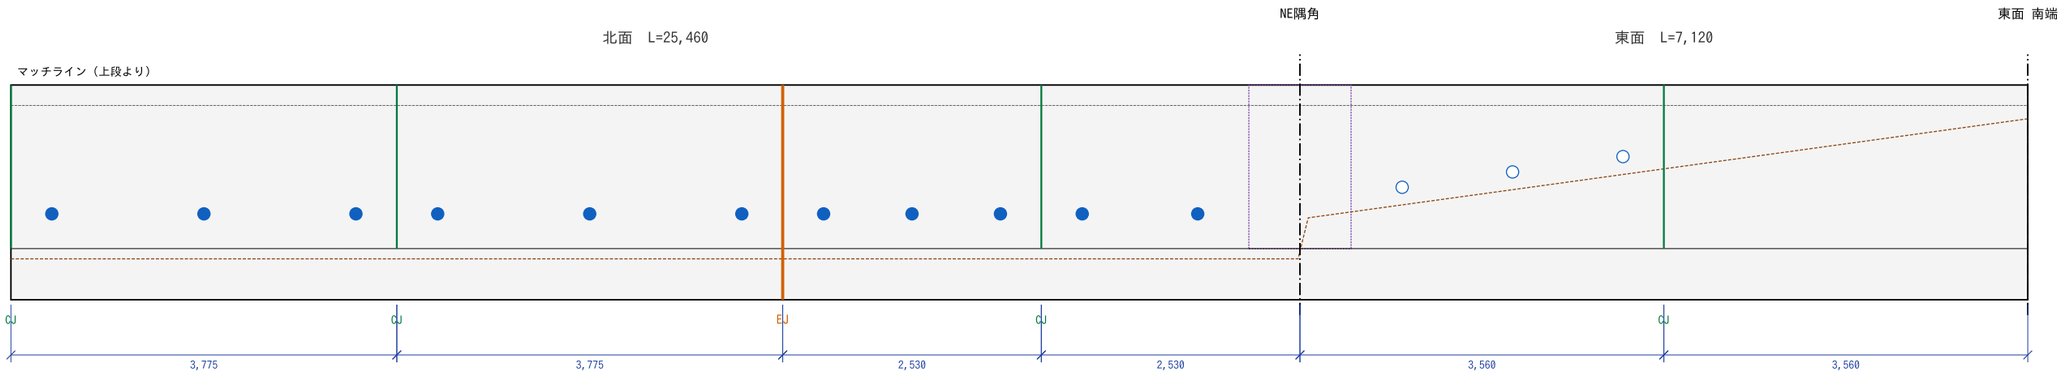

凡例・注記

EJ	伸縮目地：底盤まで全断面縁切り（エラスタイト t=10＋外面シーリング）
CJ	誘発目地：立上り両面 目地棒 30/20×D25（天端～底盤天）
●	水抜穴 VP75 標準高さ ±0-1060（管底＝止水コン天端）
○	水抜穴 調整高さ＝外部地盤+150（止水コンも同高さに上げる）
- -	外部地盤（嵩上げ後）：北 -1500（既存-1660～-1680を嵩上げ）／西（帯状部・仮定）NW隅1.5mまで-1500→南端-210／東 -1110→-130
□	隅角部ハンチ 500×500 範囲

・天端は ±0+200 で水平（各点の現況GL：A-1/B-1 +57, B-3 +60, B-4 +50, B-5 +100, C-1 ±0, D-1 +25）。
・底盤下端 ±0-1900 で水平。BMは配置図 ±0 とし、着工前にレベル確認。
・型枠：北面・東面の外面は境界線上。外部側作業スペースは隣地・道路管理者と事前協議。
・西面は境界から2,929内側（改3）。外面側の帯状部に電柱あり：電柱周囲1.0mは掘削・盛土・資材仮置き禁止（S-06）。
・型枠締付け：セパレーター＋Pコン（外面はPコン穴モルタル充填）。
・水抜穴は型枠に VP75 を仕込み、外部へ 2% 以上の下り勾配で固定。

工事名 大信薬局様邸新築工事	ハゼモト建設株式会社 一級建築士事務所 北九州市小倉北区片野4-12-10　TEL 093-931-0521　FAX 093-931-0927	管理者 櫨本 健一	設計者	担当者	図面名 擁壁 展開図	図面No S-04
備考 鉄筋・型枠・土工 協力業者配布用 改3 2026/11/05 電柱回避：西面を3.0m敷地側へ移動（北面3.0m短縮）／断面は構造計算どおり		日付 2026/11/05	日付	日付	縮尺 1/60	施工図

鉄筋加工帳（D13・D10　SD295）

符号	名称	径	形状	加工寸法(mm)	1本長	本数	総長m	重量kg	備考
W1	壁縦筋（背面・主筋）	D13	L形	1890+400	2,290	142	325.2	324	@300
W2	壁縦筋（前面）	D13	L形	1890+300	2,190	142	311.0	309	@300
W3	壁横筋（両面×6段）	D13	直	定尺6.0m	5,968	97	578.9	576	継手72箇所（40d）
W4	巾止め筋	D10	S形	90+フック	300	74	22.2	12	@1000×1000
F1	底盤上端主筋	D13	コ形(下向)	300+2787+300	3,387	142	481.0	479	@300
F2	底盤下端主筋	D13	コ形(上向)	300+2759+300	3,359	142	477.0	475	@300
F3	底盤配力筋（上下×10本）	D13	直	定尺6.0m	5,993	161	964.8	960	継手120箇所（40d）
C1a	NW隅 ハンチ斜め筋	D13	折曲げ	520+780+520	1,820	6	10.9	11	
C1b	NE隅 ハンチ斜め筋	D13	折曲げ	520+567+520	1,607	6	9.6	10	
C2	ハンチ縦補強筋	D13	L形	1890+300	2,190	6	13.1	13	各隅3本
C3	隅角 内側横筋定着	D13	L形	延長+520	520	24	12.5	12	各隅6段×2面
E1	端部コ字筋（壁）	D13	コ形	520+90+520	1,130	12	13.6	13	2端部×6段
E2	端部縦筋 追加	D13	L形	1890+300	2,190	4	8.8	9	2端部×2本

鉄筋合計（概算・ロス別）　約 3,203 kg　≒ 3.20 t　（D13 0.995kg/m、D10 0.560kg/m）

※本数は壁延長を伸縮目地・隅角で区切った区間毎に @300 で算出（区間：西9.90 / 北5.30・15.10・5.06 / 東7.12 m）。現場で端数調整のこと。

※曲げ加工寸法は外寸。縦筋の上端は天端かぶり80で直止め。重ね継手40d(520)は千鳥配置、隅角部・目地部に継手を設けない。


コンクリート・型枠ほか 数量（概算）

項目	数量	単位	備考
擁壁延長（外面）	42.48	m	西9.90＋北25.46＋東7.12（改3）
コンクリート 底盤 t=500	53.07	m^3	底盤面積 106.1m^2
コンクリート 立上り t=250（ハンチ含）	17.14	m^3	H=1,600
コンクリート 計 Fc21	70.21	m^3	ロス別
均しコンクリート t=50	5.57	m^3	敷地側100出し
基礎砕石 t=100	11.15	m^3	転圧
型枠（外面・内面・妻）	181	m^2	伸縮目地妻型枠含む
裏込砕石 300×800	9.9	m^3	
止水コンクリート 350×50	0.72	m^3	
面木 20×20	92	m	天端両角＋端部・出隅
目地棒 30/20×D25（誘発目地）	25.6	m	8箇所×両面
エラスタイト t=10（伸縮目地）	3.8	m^2	2箇所
シーリング 10×10	17.5	m	外面・天端
前面ふかしコン W300（無筋 Fc18）	3.27	m^3	北面全長＋西面1.5m
前面嵩上げ盛土（転圧）	5.5	m^3	平均17cm×幅約1.2m 概算
水抜穴 VP75 L=300	31	箇所	吸出し防止材共

着工前 確認事項（監督・設計者）

1. 根入れ：躯体は構造計算どおり（底盤下端 ±0-1900）。北面・西面NW側の前面地盤を ±0-1500 に嵩上げ＋前面ふかしコン W300 で根入れ400を確保。見え高さ 1,700（2m以下）。嵩上げ部は外面から1.0m以上平坦、転圧管理。
2. 天端 ±0+200 水平の可否（現況GL ±0〜+100、天端の見え高さが変わる）。
3. 西面は境界から2,929内側（北面3,000短縮）。電柱・支柱の位置を実測し新西面まで1.0m以上（推定 表面で1,904）を確認。九電と事前協議（S-06）。帯状部（旧西面位置〜新西面）の仕上げ高さ・排水・土留めを決定。
4. 外部地盤高さを実測し、水抜穴の高さ（標準／調整／省略）を確定。
5. 申請建物基礎と北面底盤（ヒール）の重なり・取合い高さ。
6. 外面型枠・足場の作業スペース（隣地承諾・道路使用）。
7. 東面（道路側）は既存地盤で根入れ790以上のため嵩上げ不要。上空線（電線）の高さを実測、重機・ポンプ車の作業高さを制限（S-06）。
8. 数量・本数は概算。鉄筋業者にて加工帳を最終チェックのこと。


形状略図

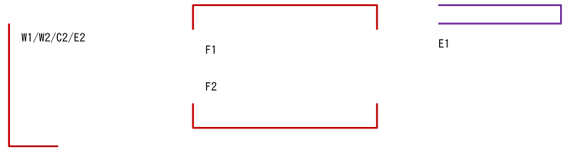

工事名 大信薬局様邸新築工事	ハゼモト建設株式会社 一級建築士事務所 北九州市小倉北区片野4-12-10　TEL 093-931-0521　FAX 093-931-0927	管理者 櫨本 健一	設計者	担当者	図面名 擁壁 鉄筋加工帳・数量表	図面No S-05
備考 鉄筋・型枠・土工 協力業者配布用 改3 2026/11/05 電柱回避：西面を3.0m敷地側へ移動（北面3.0m短縮）／断面は構造計算どおり		日付 2026/11/05	日付	日付	縮尺 —	施工図


電柱回避・建柱車 施工検討図　　平面 S=1/150 ／ 断面 S=1/150

① 平面（電柱・上空線・掘削範囲・建柱車据付候補）

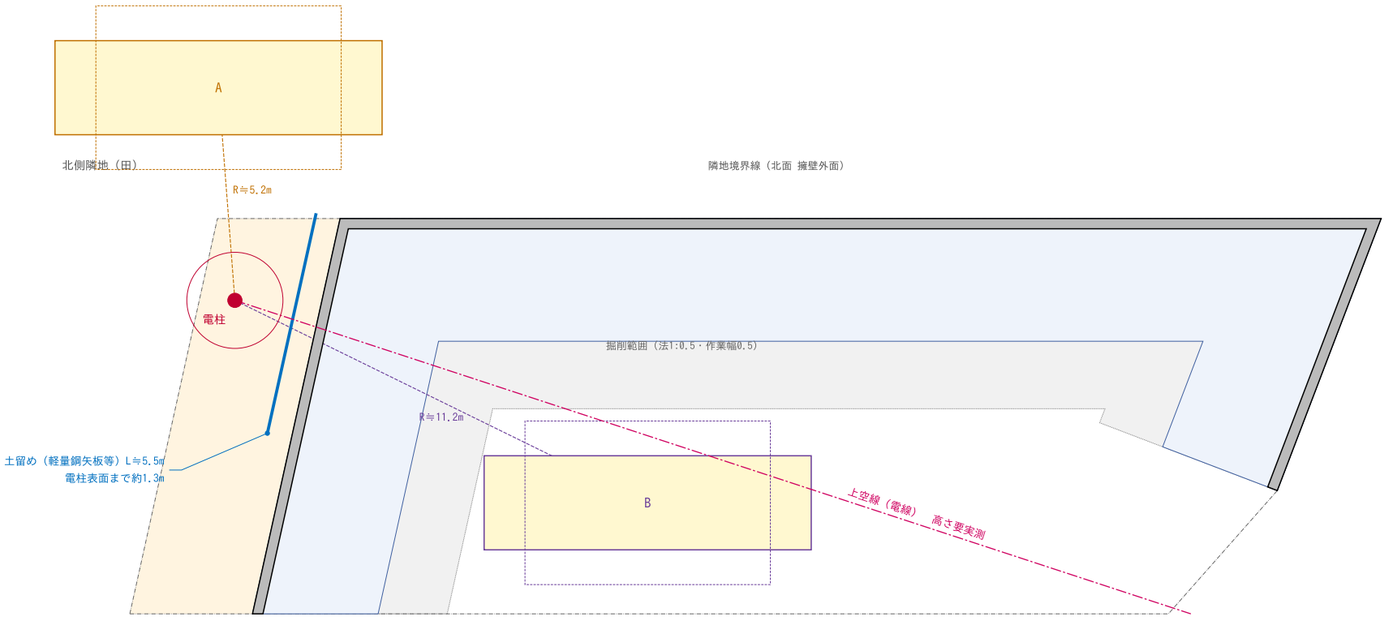

建柱車は代表寸法（全幅2.3m×全長8m、アウトリガ張出幅4m を点線）で表示。機種は九州電力の配車による。

② 断面（新西面に直角・電柱位置）　高さは推定・要実測

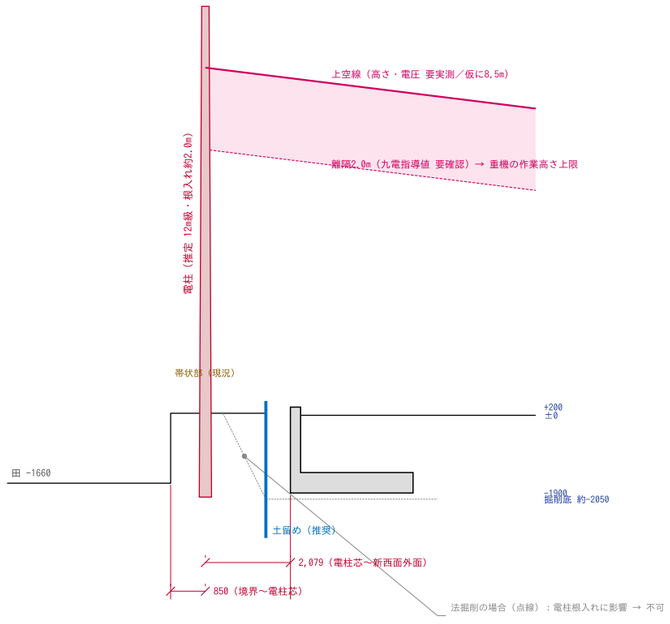

1. 前提（推定値・着工前に実測）

・電柱：西境界から850・北境界から2,000（配置図への手書き指示）。支柱付き。
・電柱 φ350・12m級・根入れ約2.0m と仮定。支柱の足元位置は未確認。
・上空線：電柱から南東へ敷地を斜めに横断（調査位置図）。
　電圧区分（高圧6.6kV／低圧／通信）・地上高さは未確認。

2. 擁壁と電柱の離れ

・新西面外面まで 芯2,079／表面1,904（必要1,000 → OK）
・法掘削（1:0.5・作業幅0.5）だと掘削天端が電柱表面から約0.25m
　→ 根入れ部の地盤を緩めるため不可。
・電柱側は土留め（軽量鋼矢板等 L≒6m）で鉛直掘削 → 電柱表面まで約1.3m。
　支柱足元が土留め範囲に入る場合は位置を見直す。

3. 建柱車による電柱支持（九電作業）の可否

据付位置	電柱まで	課題	判定
A 北側隣地（田）	約5.2m	敷鉄板・進入路・地権者承諾	○ 条件付
B 敷地内（掘削範囲外）	約11m	掘削範囲が広く遠い・上空線の下	× 実質不可
C 帯状部（旧西面～新西面）	約2.3m幅	車幅＋アウトリガが入らない	× 不可
D 南側道路	約9m以上	道路使用許可・作業半径大	△

4. 上空線の下での作業（当社・協力業者）

・重機・ポンプ車・ユニック：電線から2.0m以上（九電指導値）。
　法定の最小離隔（基発第759号）：低圧1.0m／高圧1.2m。
・九電に防護管の取付を依頼。上空線の下では監視人を配置する。
・上空線の下は小旋回機（0.1～0.25m³）で作業高さを制限して使う。
・生コンはポンプ車のブームが上空線にかからない位置から打設する。

5. 結論（推奨）

①電柱側は土留めで掘削し、電柱支持（建柱車）を不要にする。
②九電が支持を求めた場合は、北側隣地（A）に敷鉄板を敷いて据付。
③着工前に九電と現地立会い：電柱・支柱・電線の位置と高さ、
　支持の要否、防護管、作業日程、費用負担を確認する。

工事名 大信薬局様邸新築工事	ハゼモト建設株式会社 一級建築士事務所 北九州市小倉北区片野4-12-10　TEL 093-931-0521　FAX 093-931-0927	管理者 櫨本 健一	設計者	担当者	図面名 電柱回避・建柱車 施工検討図	図面No S-06
備考 鉄筋・型枠・土工 協力業者配布用 改3 2026/11/05 電柱回避：西面を3.0m敷地側へ移動（北面3.0m短縮）／断面は構造計算どおり		日付 2026/11/05	日付	日付	縮尺 1/150	施工図