

(5) コラム伏図

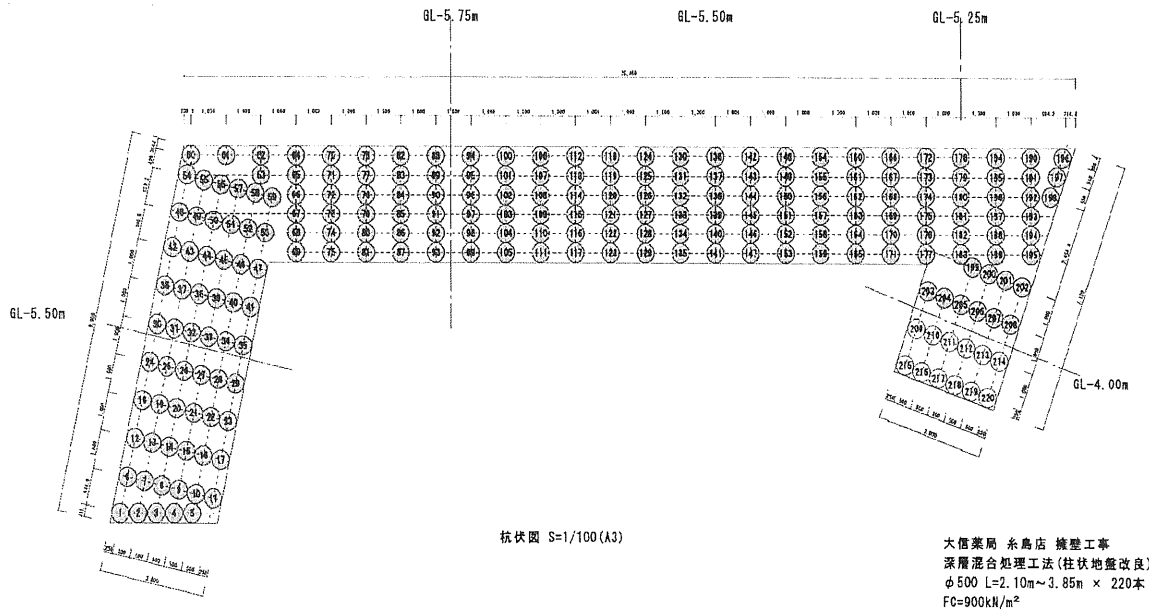

杭伏図 S=1/100(A3)

大信薬局 糸島店 擁壁工事
深層混合処理工法(柱状地盤改良)
φ500 L=2.10m～3.85m × 220本
FC=900kN/m²
添加量300kg/m³
固化材：TL-3E(六価クロム溶出低減型)

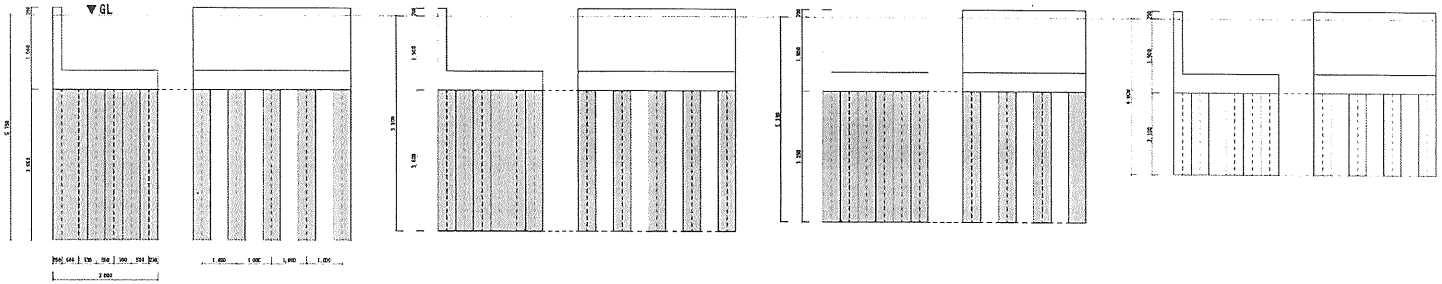

改良径 φ500
掘削長：5.75m
空　掘：1.90m
改良長：3.85m

改良体本数：70本

改良体径 φ500
掘削長：5.50m
空　掘：1.90m
改良長：3.60m

改良体本数：89本

改良体径 φ500
掘削長：5.25m
空　掘：1.90m
改良長：3.35m

改良体本数：49本

改良体径 φ500
掘削長：4.00m
空掘長：1.90m
改良長：2.10m

改良体本数：12本